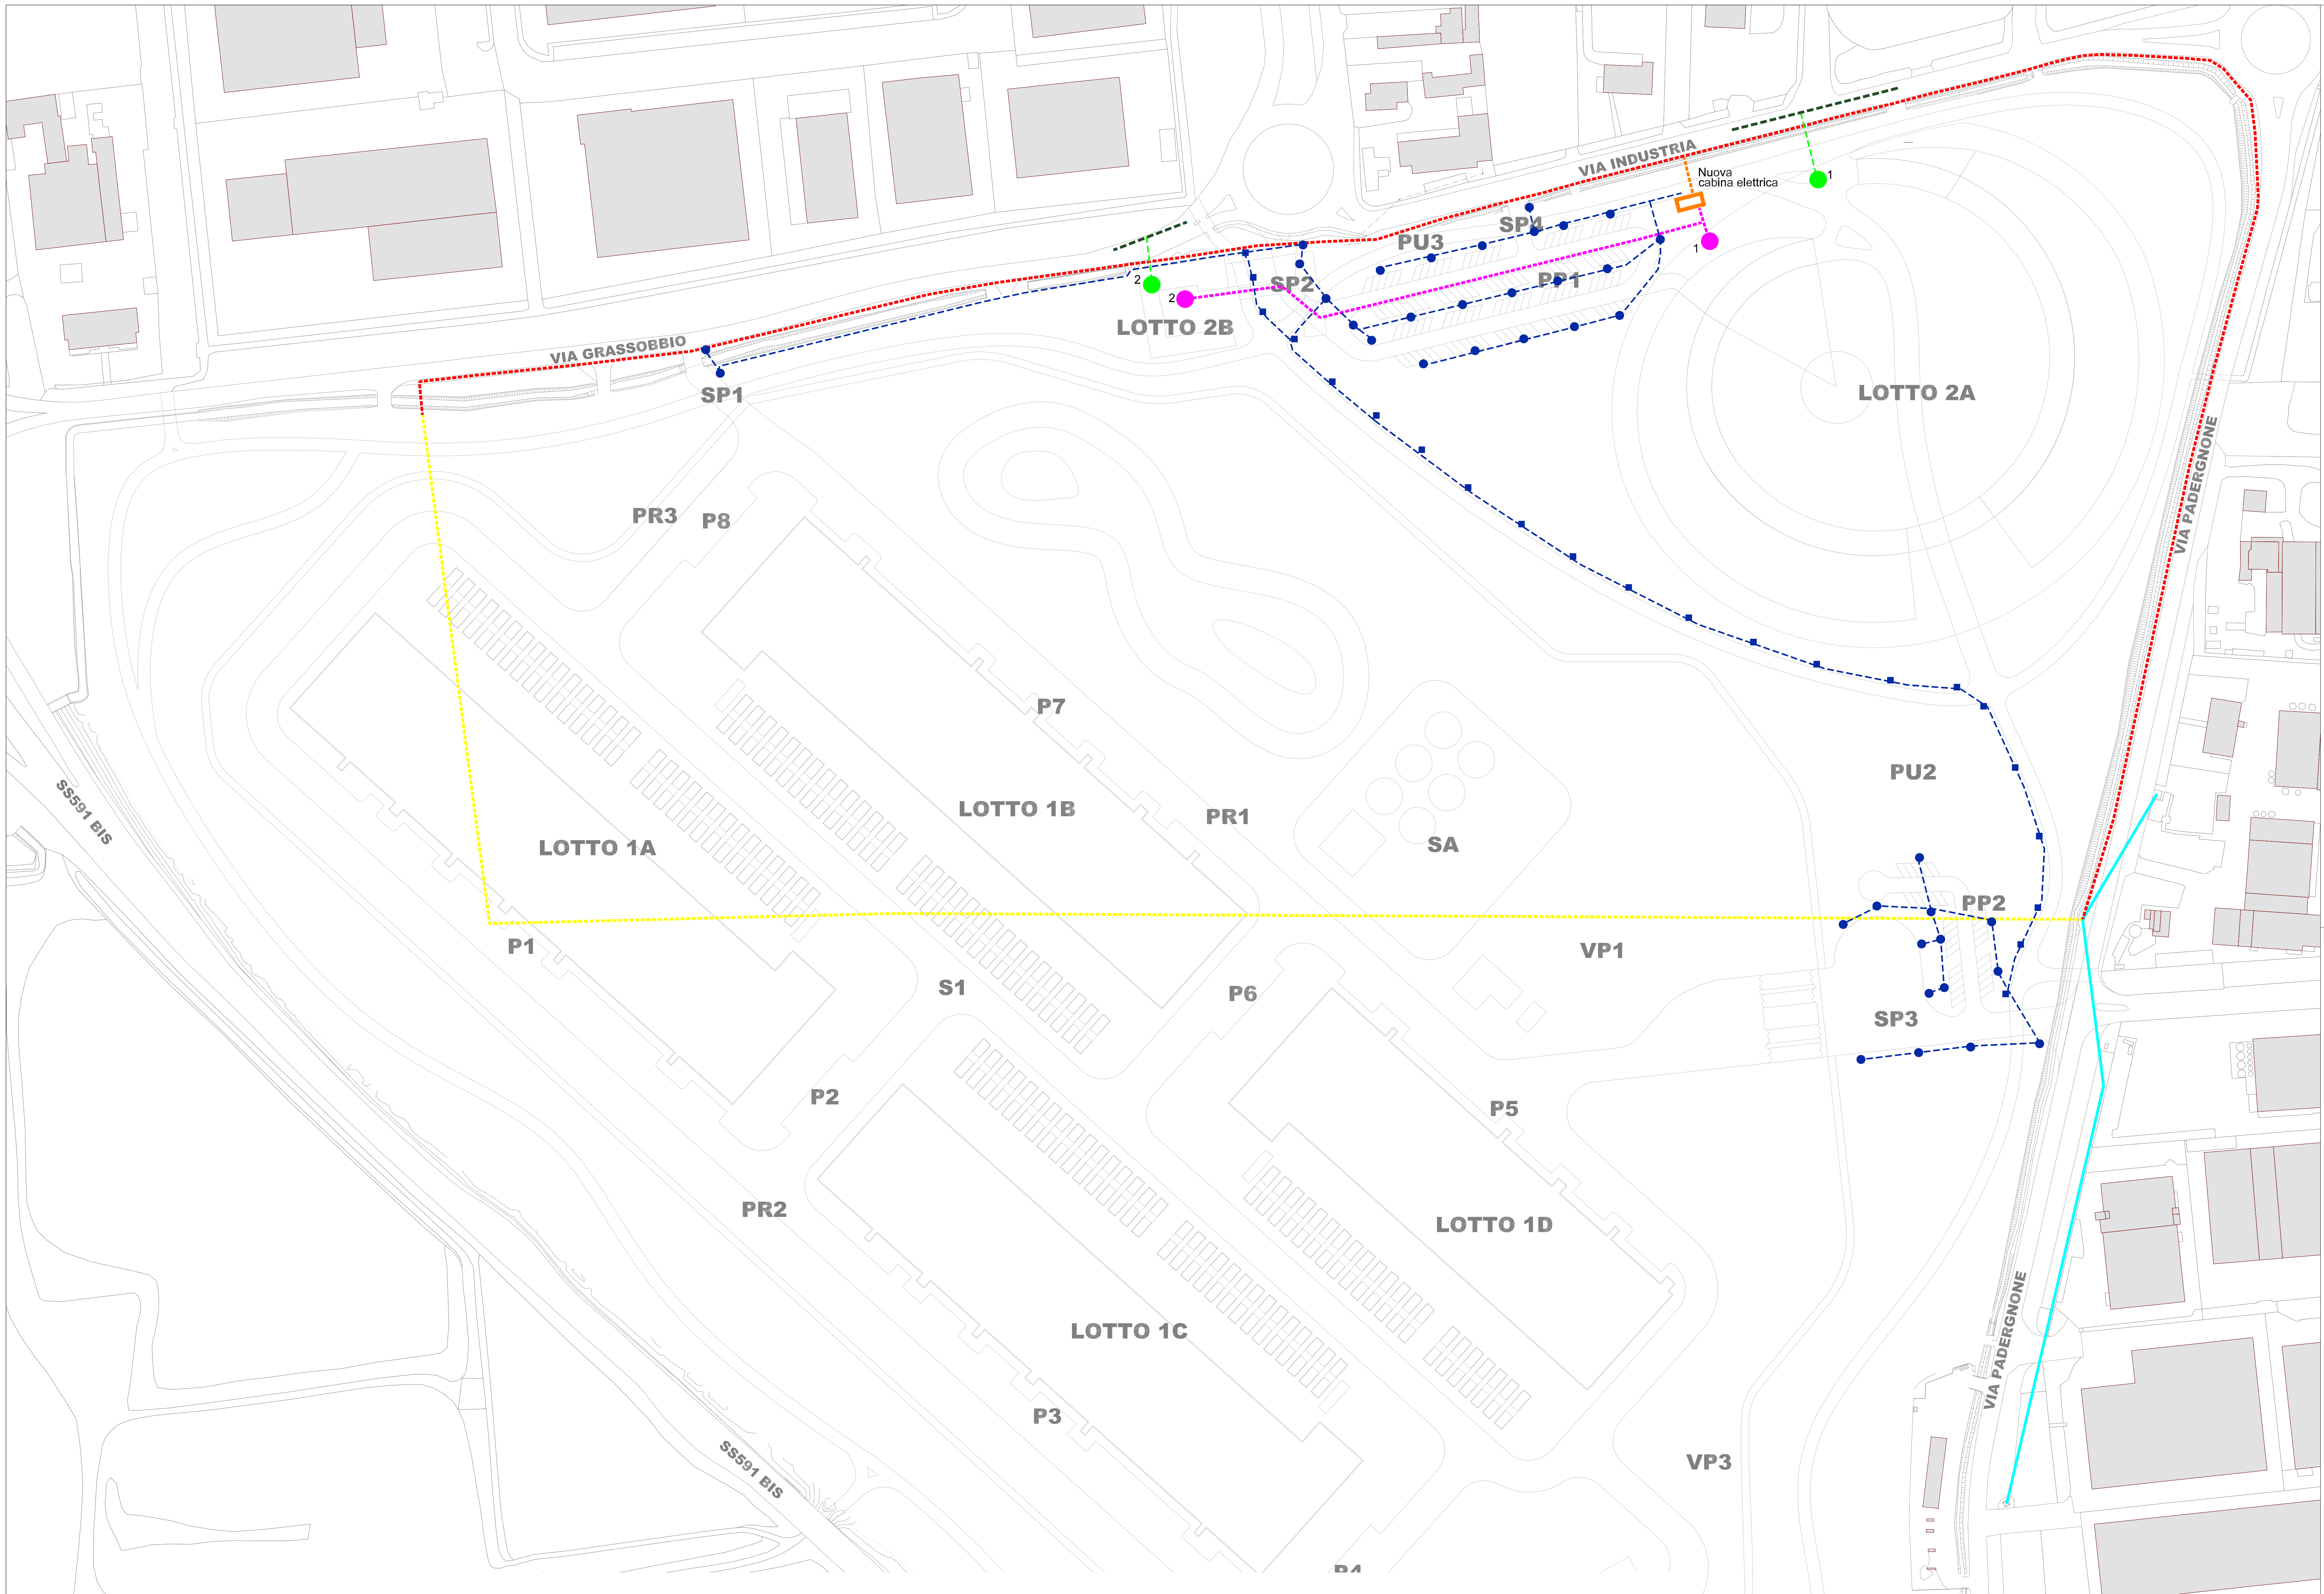

Reti elettriche esistenti

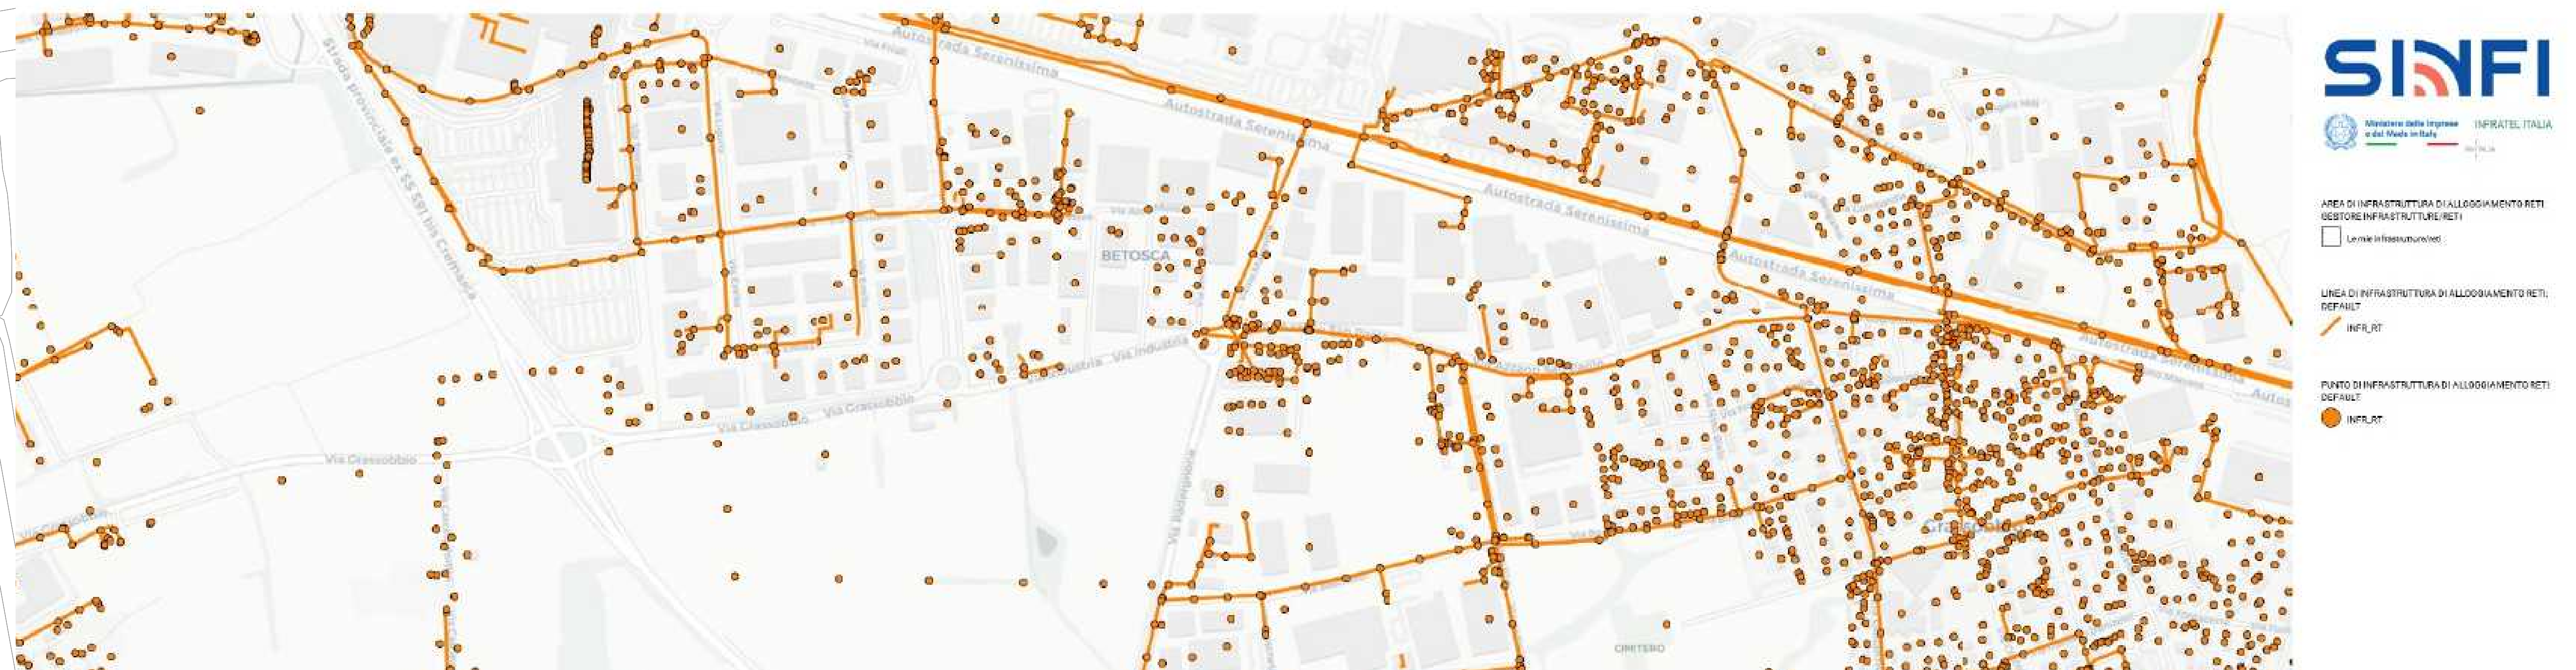
SINFI
Ministero delle Imprese e del Made in Italy
INFRATEL ITALIA
AREA DI INFRASTRUTTURA DI ALLOGGIAMENTO RETI
GESTORE INFRASTRUTTURE/RETI
Le mie infrastrutture/reti
LINEA DI INFRASTRUTTURA DI ALLOGGIAMENTO RETI
DEFAULT
INFR_RT
PUNTO DI INFRASTRUTTURA DI ALLOGGIAMENTO RETI
DEFAULT
INFR_RT

LEGENDA

🟥	Perimetro Ambito

RETE ELETTRICA

▬	Linea Enel media tensione tratto esistente confermato	▭	Nuova cabina di trasformazione al servizio Tech Hub
┅	Linea Enel Media tensione tratto esistente da eliminare	┅	Linea di distribuzione interna (privata)
┅	Linea Enel Media tensione nuovo tratto interrato	● 1-3	Punti di allaccio edifici privati
┅	Nuova linea di servizio al Tech Hub		

NB. La cabina elettrica viene dimensionata per l'intero intervento tech hub, ma sarà attrezzata con i trasformatori in funzione del programma di costruzione

Le strutture del Data Center sono alimentate direttamente dalla sottostazione elettrica e non dalla rete elettrica

RETE ILLUMINAZIONE PUBBLICA

╌	Nuova linea pubblica illuminazione allaccio quadro da nuova cabina Enel		
●	Punto luce tipo carrale	■	Punto luce tipo pedonale

RETE TELECOMUNICAZIONI

╌	Nuova linea pubblica illuminazione allaccio quadro da nuova cabina Enel	╌	Rete telecomunicazioni pubblica
●	Punto allaccio privato		

ACCORDO DI PROGRAMMA

RIGENERAZIONE URBANA E TERRITORIALE
DELL'EX AMBITO ESTRATTIVO DEL PADERGNONE

NUOVO POLO TECNOLOGICO DI INTERESSE SOVRALOCALE

PROVINCIA DI BERGAMO
Via Torquato Tasso 8
24121 Bergamo
PEC protocollo@pec.provincia.bergamo.it
Tel 035387111

COMUNE DI ZANICA
Via Roma 35
24050 Zanica
PEC protocollo@pec.comune.zanica.bg.it
Tel 0354245811

PROMOTORE
Real Estate SPV Project 2415 S.r.l.
Corso Vittorio Emanuele II No. 24/28
20122 – Milano (Italia)
PEC realestatespvproject2415@legalmail.it
Tel +39 02 7788051 -

F - OPERE DI URBANIZZAZIONE

SCALA 1:1000	DATA SETTEMBRE 2026		
TITOLO TAVOLA **SCHEMA DI MASSIMA URBANIZZAZIONI RETE ELETTRICA RETE ILLUMINAZIONE PUBBLICA RETE TELECOMUNICAZIONI**	NUMERO TAVOLA **F1**	AGGIORN. AGGIORN. AGGIORN.	N

TAVOLO TECNICO ISTITUZIONALE

COMUNE DI ZANICA:
UFFICIO URBANISTICA EDILIZIA PRIVATA E SUE
Dirigente
Dott. arch. Gianluca Della Mea
gianluca.dellamea@comune.zanica.bg.it
tel. 035 4245811 int 3

PROGETTISTI E CONSULENTI

PROGETTO URBANISTICO E COORDINAMENTO GENERALE
Marcello Fiorina - ingegnere
Elisabetta Nani - ingegnere
Studio associato di architettura urbanistica ed ingegneria
Sede in via pignolo 5, Bergamo tel 035-218094 - 035-270308
www.studiofiorina.com - indirizzo email: info@studiofiorina.com

PAESAGGIO AMBIENTE E NATURA
STUDIO GERUNDO
Studio Gerundo
Arch. Paolo Pelliccioli
Ing. Susanna Quirico
Dott. Agr. Alberto Massa Saluzzo
Via Cagnola 25 – Treviglio
Tel 3475331955 e-mail: info@studiogerundo.it

TECH CONCEPT AND ARCHITECTURAL
RKD
Kevin Maguire
Derek Meenan
The Eight Building
Dublin - Ireland - D08 T2TX
Tel +353 1 668 1055 e-mail: mail@rkd.ie
https://www.rkd.ie

TECH CONCEPT AND ARCHITECTURAL
BEAST Design Studios GmbH
Gustavo Espigado
Kölner Str. 1
Eschborn - Germany - 65760
Tel +49 (0) 6196 7700 410
e-mail: g.espigado@beastdesignstudios.com
www.beastdesignstudios.com

ENGINEERING AND INFRASTRUCTURE
ETS Engineering and Technical Services SpA
Donato Romano
Via Angelo Mazzi, 32
Villa d'Almè - Bergamo - 24018
Tel +39 035 6313111 e-mail: info@etseng.it
https://www.etseng.it/

TRASPORTI, AMBIENTE, INVARIANZA IDRAULICA
TE.A. CONSULTING SRL
ING. MASSIMO MOI
MI Via G.B. Grassi 15 - 20157 Milano (MI)
T 02 21711067
BG Via Don A. Mazzucotelli 6 - 24020 Gorle (BG)
T 035 321360
www.territorioambiente.com

VALUTAZIONE AMBIENTALE STRATEGICA
TE.A. CONSULTING SRL
ING. MASSIMO MOI
MI Via G.B. Grassi 15 - 20157 Milano (MI)
T 02 21711067
BG Via Don A. Mazzucotelli 6 - 24020 Gorle (BG)
T 035 321360
www.territorioambiente.com

POWER AND INFRASTRUCTURE
H&MV Engineering
Paul O'Helleran, Fabio Sbacches
Hamilton House Block 2
Castletroy - Ireland - V94 YHD6
Tel +35 36 135 7496 e-mail: info@hmvengineering.com
https://www.hmvengineering.com/