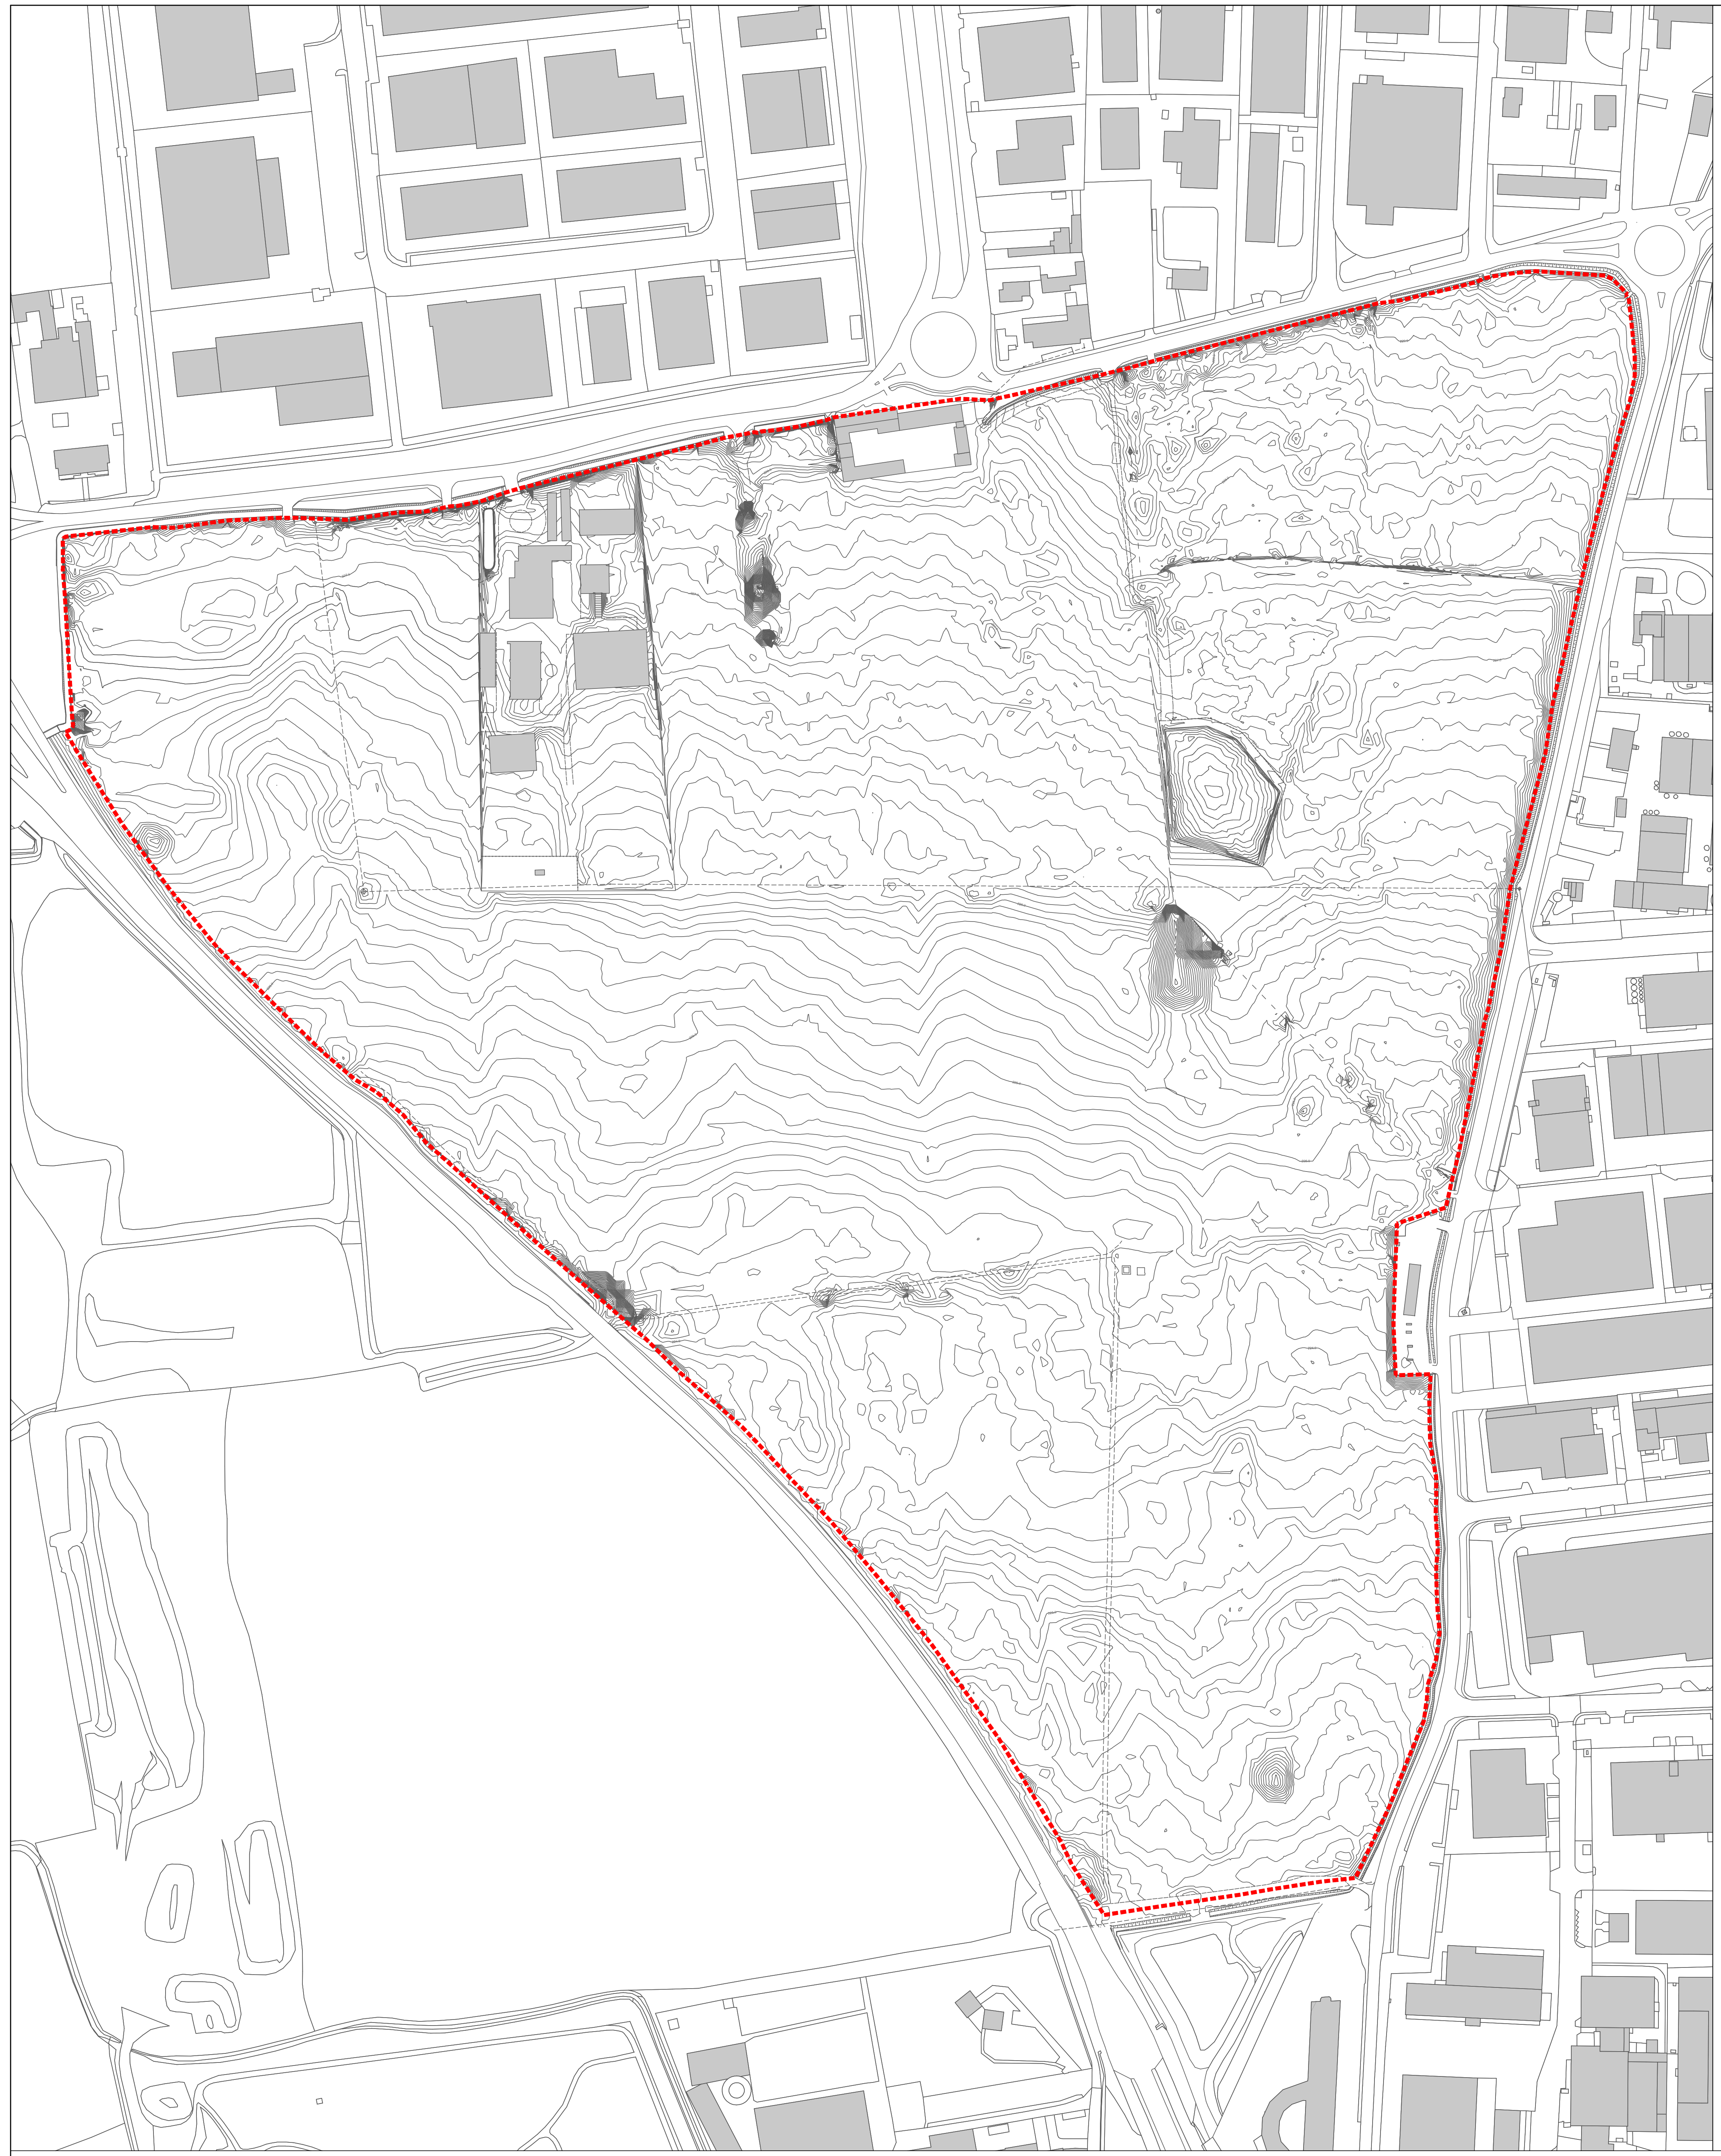

STATO DI FATTO: PLANIMETRIA GENERALE AREA DI INTERVENTO

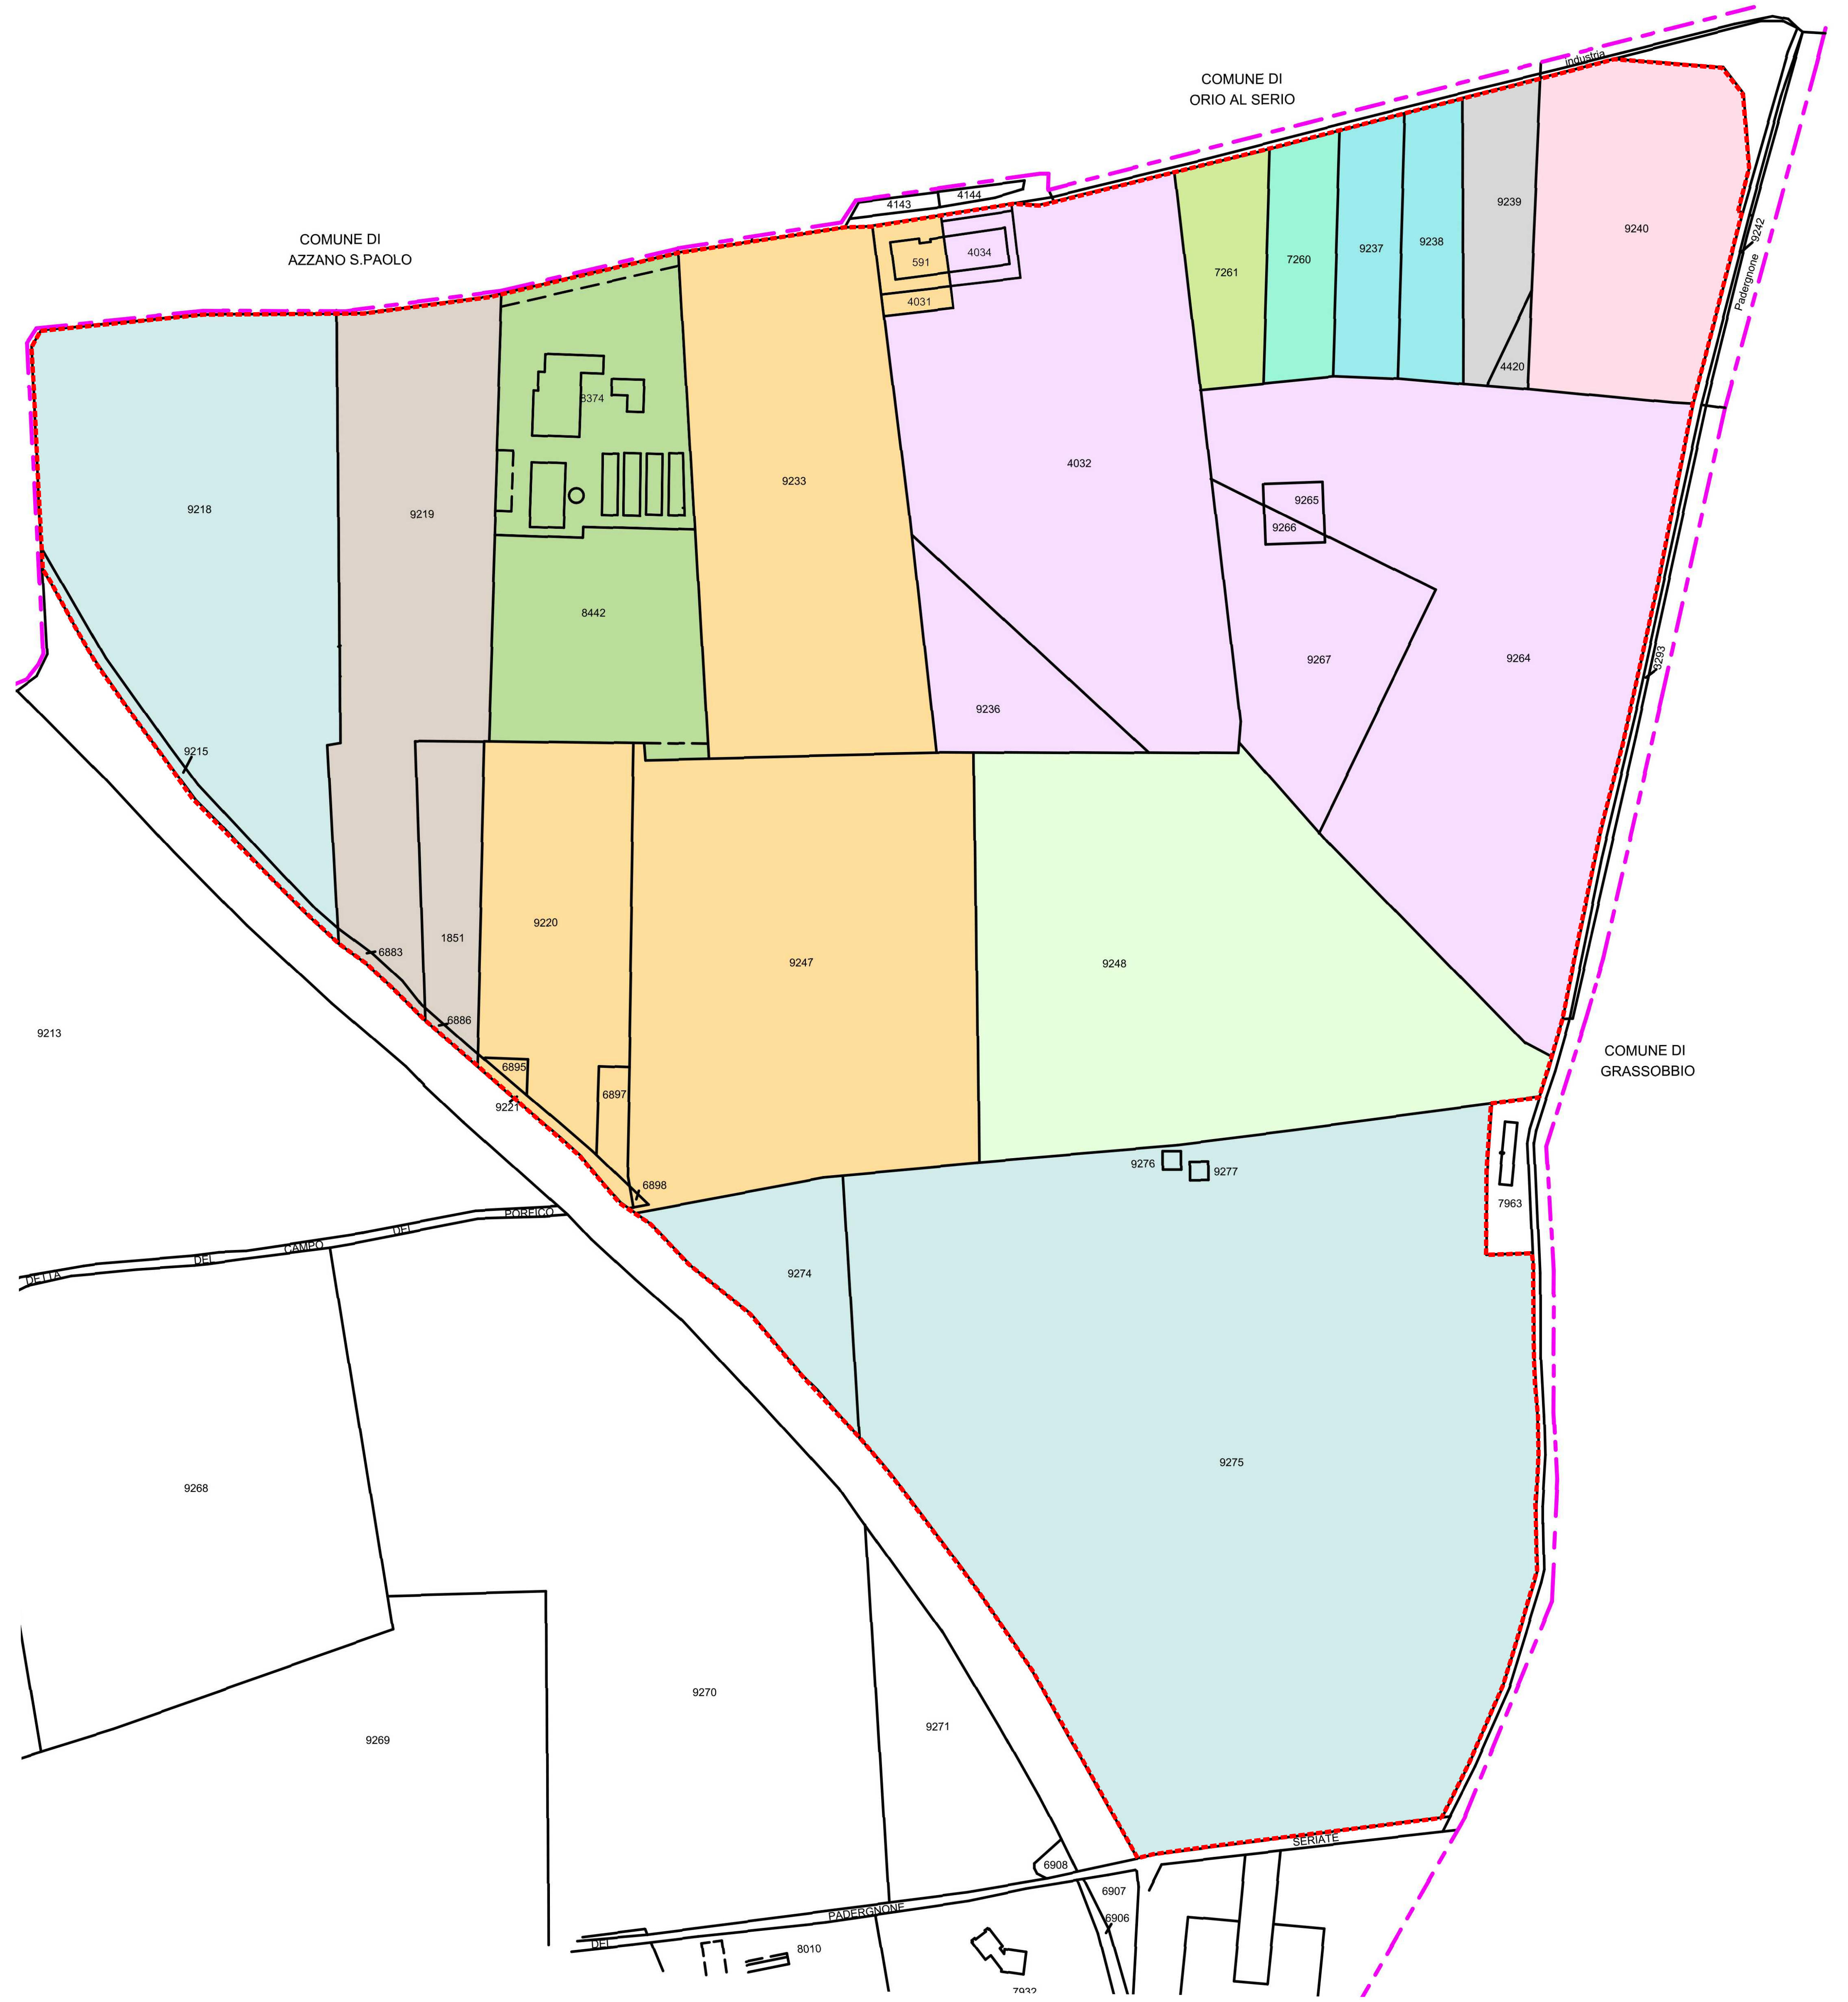

STATO DI FATTO: ESTRATTO MAPPA CATASTALE

ELENCO PRPRIETÀ E MAPPALI INTERESSATI DALL'ACCORDO DI PROGRAMMA

CATASTO	FOGLIO	PARTICELLA	SUB	QUALITA' / CATEGORIA	PROPRIETÀ
TERRENI	1	9218		SEMINATIVO	**NUOVA DEMI SpA**
TERRENI	1	9215		SEMINATIVO	
TERRENI	1	9274		SEMINATIVO	
TERRENI	1	9275		SEMINATIVO	
TERRENI	1	9276		FABBRICATO URBANO DA ACCERTARE	
TERRENI	1	9277		FABBRICATO URBANO DA ACCERTARE	
TERRENI	1	9248		SEMINATIVO IRRIGUO	**PETRA SpA**
TERRENI	1	4032		SEMINATIVO IRRIGUO ARBORATO	EX **COMELLI ALDA, COMELLI ELENA** OGGI Real Estate SPV Project 2415 S.r.l.
TERRENI	1	9236		SEMINATIVO IRRIGUO	
TERRENI	1	9264		SEMINATIVO IRRIGUO ARBORATO	
TERRENI	1	9265		FABBRICATO URBANO DA ACCERTARE	
TERRENI	1	9266		FABBRICATO URBANO DA ACCERTARE	
TERRENI	1	9267		SEMINATIVO IRRIGUO ARBORATO	
FABBRICATI	1	4034	2	A/4	
FABBRICATI	1	4034	3	C/2	
FABBRICATI	1	4034	1	BCNC	
TERRENI	1	9239		SEMINATIVO IRRIGUO ARBORATO	**CMB COSTRUZIONI SRL**
TERRENI	1	4420		SEMINATIVO IRRIGUO ARBORATO	
TERRENI	1	8442			**CROTTI EMILIO**
FABBRICATI	1	8374	701	A/7	
FABBRICATI	1	8374	702	C/6	
FABBRICATI	1	8374	703	C/7	
FABBRICATI	1	8374	704	D/10	
TERRENI	1	9237		OGGI Real Estate SPV Project 2415 S.r.l.	EX **FACCHETTI MARIA**
TERRENI	1	9238		OGGI Real Estate SPV Project 2415 S.r.l.	EX **FACCHETTI MAURIZIO. FACCHETTI VALTER**
TERRENI	1	7260			**FERRI ANGELO, FERRI ANTONIA, FERRI ESTERINA, FERRI LUIGI, FERRI ROBERTO**
TERRENI	1	7261			**MAGGIONI SAS**
TERRENI	1	9240		OGGI Real Estate SPV Project 2415 S.r.l.	EX **MOLLIS ANNA MARIA, MOLLIS BRUNO, MOLLIS GIORGIO**
TERRENI	1	9219		SEMINATIVO IRRIGUO ARBORATO	**NORIS ADELE, TERZI PIETRO, TERZI CATERINA, TERZI GIANCARLO**
TERRENI	1	6883		SEMINATIVO IRRIGUO	
TERRENI	1	1851		SEMINATIVO IRRIGUO ARBORATO	
TERRENI	1	6886		SEMINATIVO IRRIGUO ARBORATO	
TERRENI	1	9220		SEMINATIVO IRRIGUO	**CERIALE BRUNA, ZANCHI ANGELO, MAZZOLA MARIA ROSA, ZANCHI ROBERTA, ZANCHI EMANUELA, ZANCHI MAURO, ZANCHI GIOVANNA, ZANCHI DARIO, ZANCHI ANNALISA, ZANCHI MARIA ANTONIA, ZANCHI FRANCESCA**
TERRENI	1	6895		PASCOLO	
TERRENI	1	6897		PASCOLO	
TERRENI	1	9221		PASCOLO	
TERRENI	1	9233		SEMINATIVO IRRIGUO	
TERRENI	1	9247		SEMINATIVO IRRIGUO ARBORATO	
TERRENI	1	6898		PASCOLO	
TERRENI	1	4031		SEMINATIVO IRRIGUO	
FABBRICATI	1	591		C/2	

Real Estate SPV Project 2415 S.r.l. per tutti i mappali indicati di proprietà ha sottoscritto preliminari di compravendita

LEGENDA

- ▬ PERIMETRO ADP
- 🟦 PROPRIETA' NUOVA DEMI S.P.A.
- 🟩 PROPRIETA' PETRA S.P.A.
- 🟪 PROPRIETA' COMELLI
- 🟫 PROPRIETA' TERZI
- 🟧 PROPRIETA' ZANCHI
- 🟩 PROPRIETA' CROTTI
- 🟨 PROPRIETA' MAGGIONI S.A.S.
- 🟩 PROPRIETA' FERRI
- 🟦 PROPRIETA' FACCHETTI
- ⬜ PROPRIETA' CMB COSTRUZIONI S.R.L.
- 🟥 PROPRIETA' MOLLIS

NOTA: IL RILIEVO TOPOGRAFICO È STATO FORNITO DALLA PROPRIETÀ

ACCORDO DI PROGRAMMA

RIGENERAZIONE URBANA E TERRITORIALE DELL'EX AMBITO ESTRATTIVO DEL PADERGNONE

NUOVO POLO TECNOLOGICO DI INTERESSE SOVRALOCALE

PROVINCIA DI BERGAMO
Via Torquato Tasso 8
24121 Bergamo
PEC protocollo@pec.provincia.bergamo.it
Tel 035387111

COMUNE DI ZANICA
Via Roma 35
24050 Zanica
PEC protocollo@pec.comune.zanica.bg.it
Tel 0354245811

PROMOTORE
Real Estate SPV Project 2415 S.r.l.
Corso Vittorio Emanuele II No. 24/28
20122 – Milano (Italia)
PEC realestatespvproject2415@legalmail.it
Tel +39 02 7788051 -

D - PIANIFICAZIONE ATTUATIVA

SCALA	1:2000
DATA	LUGLIO 2026
TITOLO TAVOLA	STATO DI FATTO: PLANIMETRIA GENERALE AREA DI INTERVENTO ESTRATTO MAPPA CATASTALE PIANO PARTICELLARE
NUMERO TAVOLA	D1
AGGIORN.	
AGGIORN.	
AGGIORN.	

N

TAVOLO TECNICO ISTITUZIONALE

COMUNE DI ZANICA:
UFFICIO URBANISTICA EDILIZIA PRIVATA E SUE
Dirigente
Dott. arch. Gianluca Della Mea
gianluca.dellamea@comune.zanica.bg.it
tel. 035 4245811 int 3

PROGETTISTI E CONSULENTI

PROGETTO URBANISTICO E COORDINAMENTO GENERALE
Marcello Fiorina - ingegnere
Elisabetta Nani - ingegnere
Studio associato di architettura urbanistica ed Ingegneria
Sede in via pignolo 5, Bergamo tel 035-218094 - 035-270308
www.studiofiorina.com - indirizzo email: info@studiofiorina.com

PAESAGGIO AMBIENTE E NATURA
Studio Gerundo
Arch. Paolo Pelliccioli
Ing. Susanna Quirico
Dott. Agr. Alberto Massa Saluzzo
Via Cagnola 25 – Treviglio
Tel 3475331955 e-mail: info@studiogerundo.it

RKD
Kevin Maguire
Derek Meenan
The Eight Building
Dublin - Ireland - D08 T2TX
Tel +353 1 668 1055 e-mail: mail@rkd.ie
https://www.rkd.ie

BEAST Design Studios GmbH
Gustavo Espigado
Kölner Str. 1
Eschborn - Germany - 65760
Tel +49 (0) 6196 7700 410
e-mail: g.espigado@beastdesignstudios.com
www.beastdesignstudios.com

ETS Engineering and Technical Services SpA
Donato Romano
Via Angelo Mazzi, 32
Villa d'Almè - Bergamo - 24018
Tel +39 035 6313111 e-mail: info@etseng.it
https://www.etseng.it/

TRASPORTI, AMBIENTE, INVARIANZA IDRAULICA
TE.A. CONSULTING SRL
ING. MASSIMO MOI
MI Via G.B. Grassi 15 - 20157 Milano (MI)
T 02 21711067
BG Via Don A. Mazzucotelli 6 - 24020 Gorle (BG)
T 035 321360
www.territorioambiente.com

VALUTAZIONE AMBIENTALE STRATEGICA
TE.A. CONSULTING SRL
ING. MASSIMO MOI
MI Via G.B. Grassi 15 - 20157 Milano (MI)
T 02 21711067
BG Via Don A. Mazzucotelli 6 - 24020 Gorle (BG)
T 035 321360
www.territorioambiente.com

H&MV Engineering
Paul O'Helleran, Fabio Sbacches
Hamilton House Block 2
Castletroy - Ireland - V94 YHD6
Tel +35 36 135 7496 e-mail: info@hmvengineering.com
https://www.hmvengineering.com/