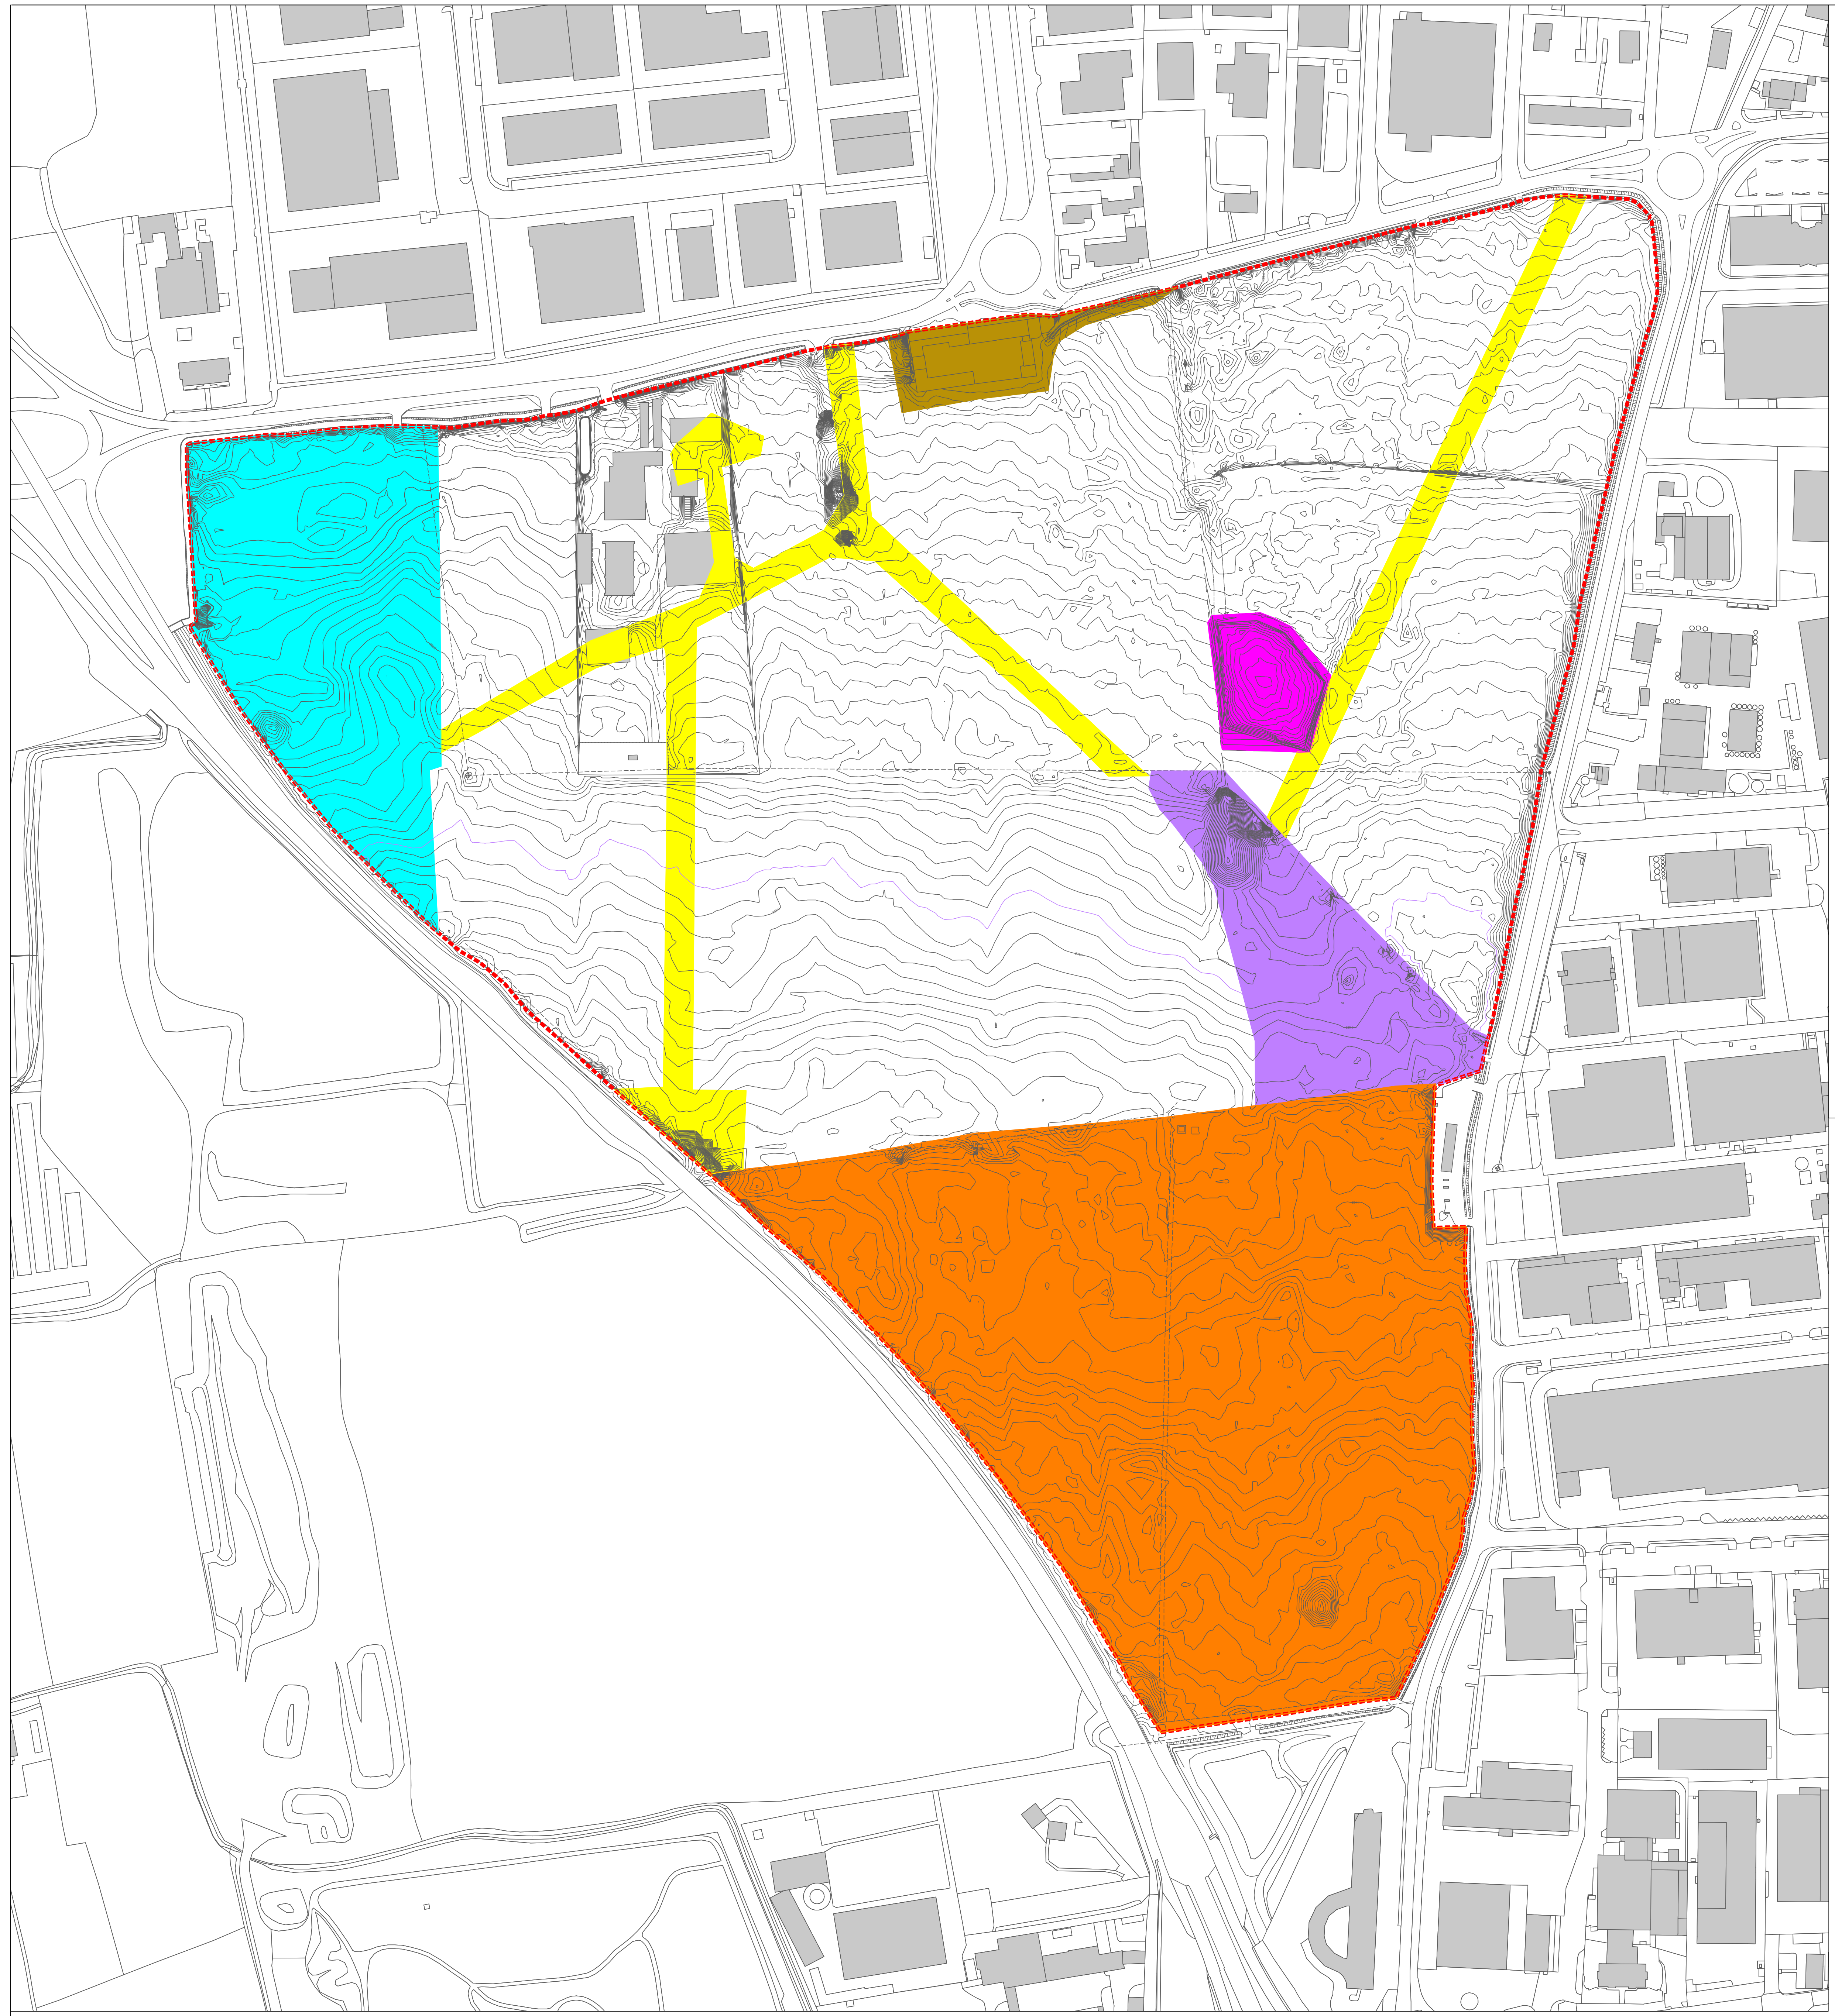

STATO DI FATTO: PLANIMETRIA GENERALE AREA DI INTERVENTO

LEGENDA

- ▭ Perimetro Ambito

🟪 Sito contaminato oggetto di bonifica ambientale con contributo di Regione Lombardia
(ex discarica Cuter)

anno 1975 - le fotografie aree mettono in luce attività di scavo e di riporto in corrispondenza dei mappali della ex cava Cuter.

anni 1970 - 1980 la depressione della ex cava Cuter è stata riempita con melme acide, generando una situazione di forte degrado e rischio ambientale. A seguito di indagini ambientali, nel 2012 è stato approvato dal Comune di Zanica un progetto di bonifica finalizzato alla rimozione delle melme acide e alla messa in sicurezza del bacino.
L'intervento ha previsto la rimozione e lo smaltimento delle melme acide e dei terreni contaminati, la realizzazione di uno strato impermeabile di isolamento e il successivo riempimento della depressione con terreno naturale, completato da una copertura impermeabile e da uno strato di terreno agricolo modellato per garantire il corretto deflusso delle acque meteoriche.
I lavori di bonifica, avviati nel 2014, si sono conclusi nel 2022. L'area oggi si presenta come un lieve dosso inerbito rispetto al piano campagna circostante.
L'intervento è stato accompagnato da un'Analisi di Rischio sito-specifica ai sensi del D.Lgs. 152/2006, valutata positivamente, che ha previsto un monitoraggio delle acque sotterranee della durata di 10 anni, attualmente in corso.

🟪 Sito oggetto di escavazione e successivo riempimento con materiali di origine antropica
discarica ante norma (ora area Petra)

anno 1975 - le fotografie aree mettono in luce attività di scavo e di riporto in corrispondenza delle aree proprietà Petra

anni successivi: la depressione, oggetto di escavazione di sabbia e ghiaia fino ad una profondità media di 8 metri dal p.c. viene successivamente riempita con terre e rocce da scavo frammiste a materiale di origine antropica (frammenti da demolizione, plastiche, legno, ecc..).

Le indagini effettuate nel sito consentono di affermare che la ex discarica individuata su parte dei terreni di proprietà Petra S.r.l. rientra nella categoria delle "discariche ante norma" in quanto si tratta di impianto antecedente all'emanazione della L.R. 7 giugno 1980
n° 94 che rappresenta la prima normativa, in Lombardia avente come scopo la gestione dei rifiuti e la definizione delle discariche; la normativa vigente, in assenza di elementi di criticità, come nel caso presente, non impone interventi specifici.

🟧 Sito oggetto di escavazione con successivo riempimento con materiali inerti
(ex discarica inerti Nuova Demi)

🟦 Cava di prestito con successivo riempimento con terre e rocce da scavo
(proprietà Nuova Demi)

anno 1998 - sono presenti attività estrattiva di sabbia e ghiaia svolte dalla ditta nuova Demi in rapporto alla costruzione della Nuova Cremasca

anni 2003 2014 - all'attività estrattiva di sabbia e ghiaia fa seguito il progressivo recupero ambientale ad uso agricolo con ripristino morfologico dei luoghi.

Ad oggi l'attività estrattiva e di successivo ripristino è conclusa e le successive analisi di monitoraggio non hanno evidenziato contaminazioni connesse all'impianto di discarica inerti.

🟨 Sedime piste di rullaggio e parcamento
ex aeroporto militare

🟫 Edifici rurali e residenziali dismessi
in stato di degrado ed abbandono

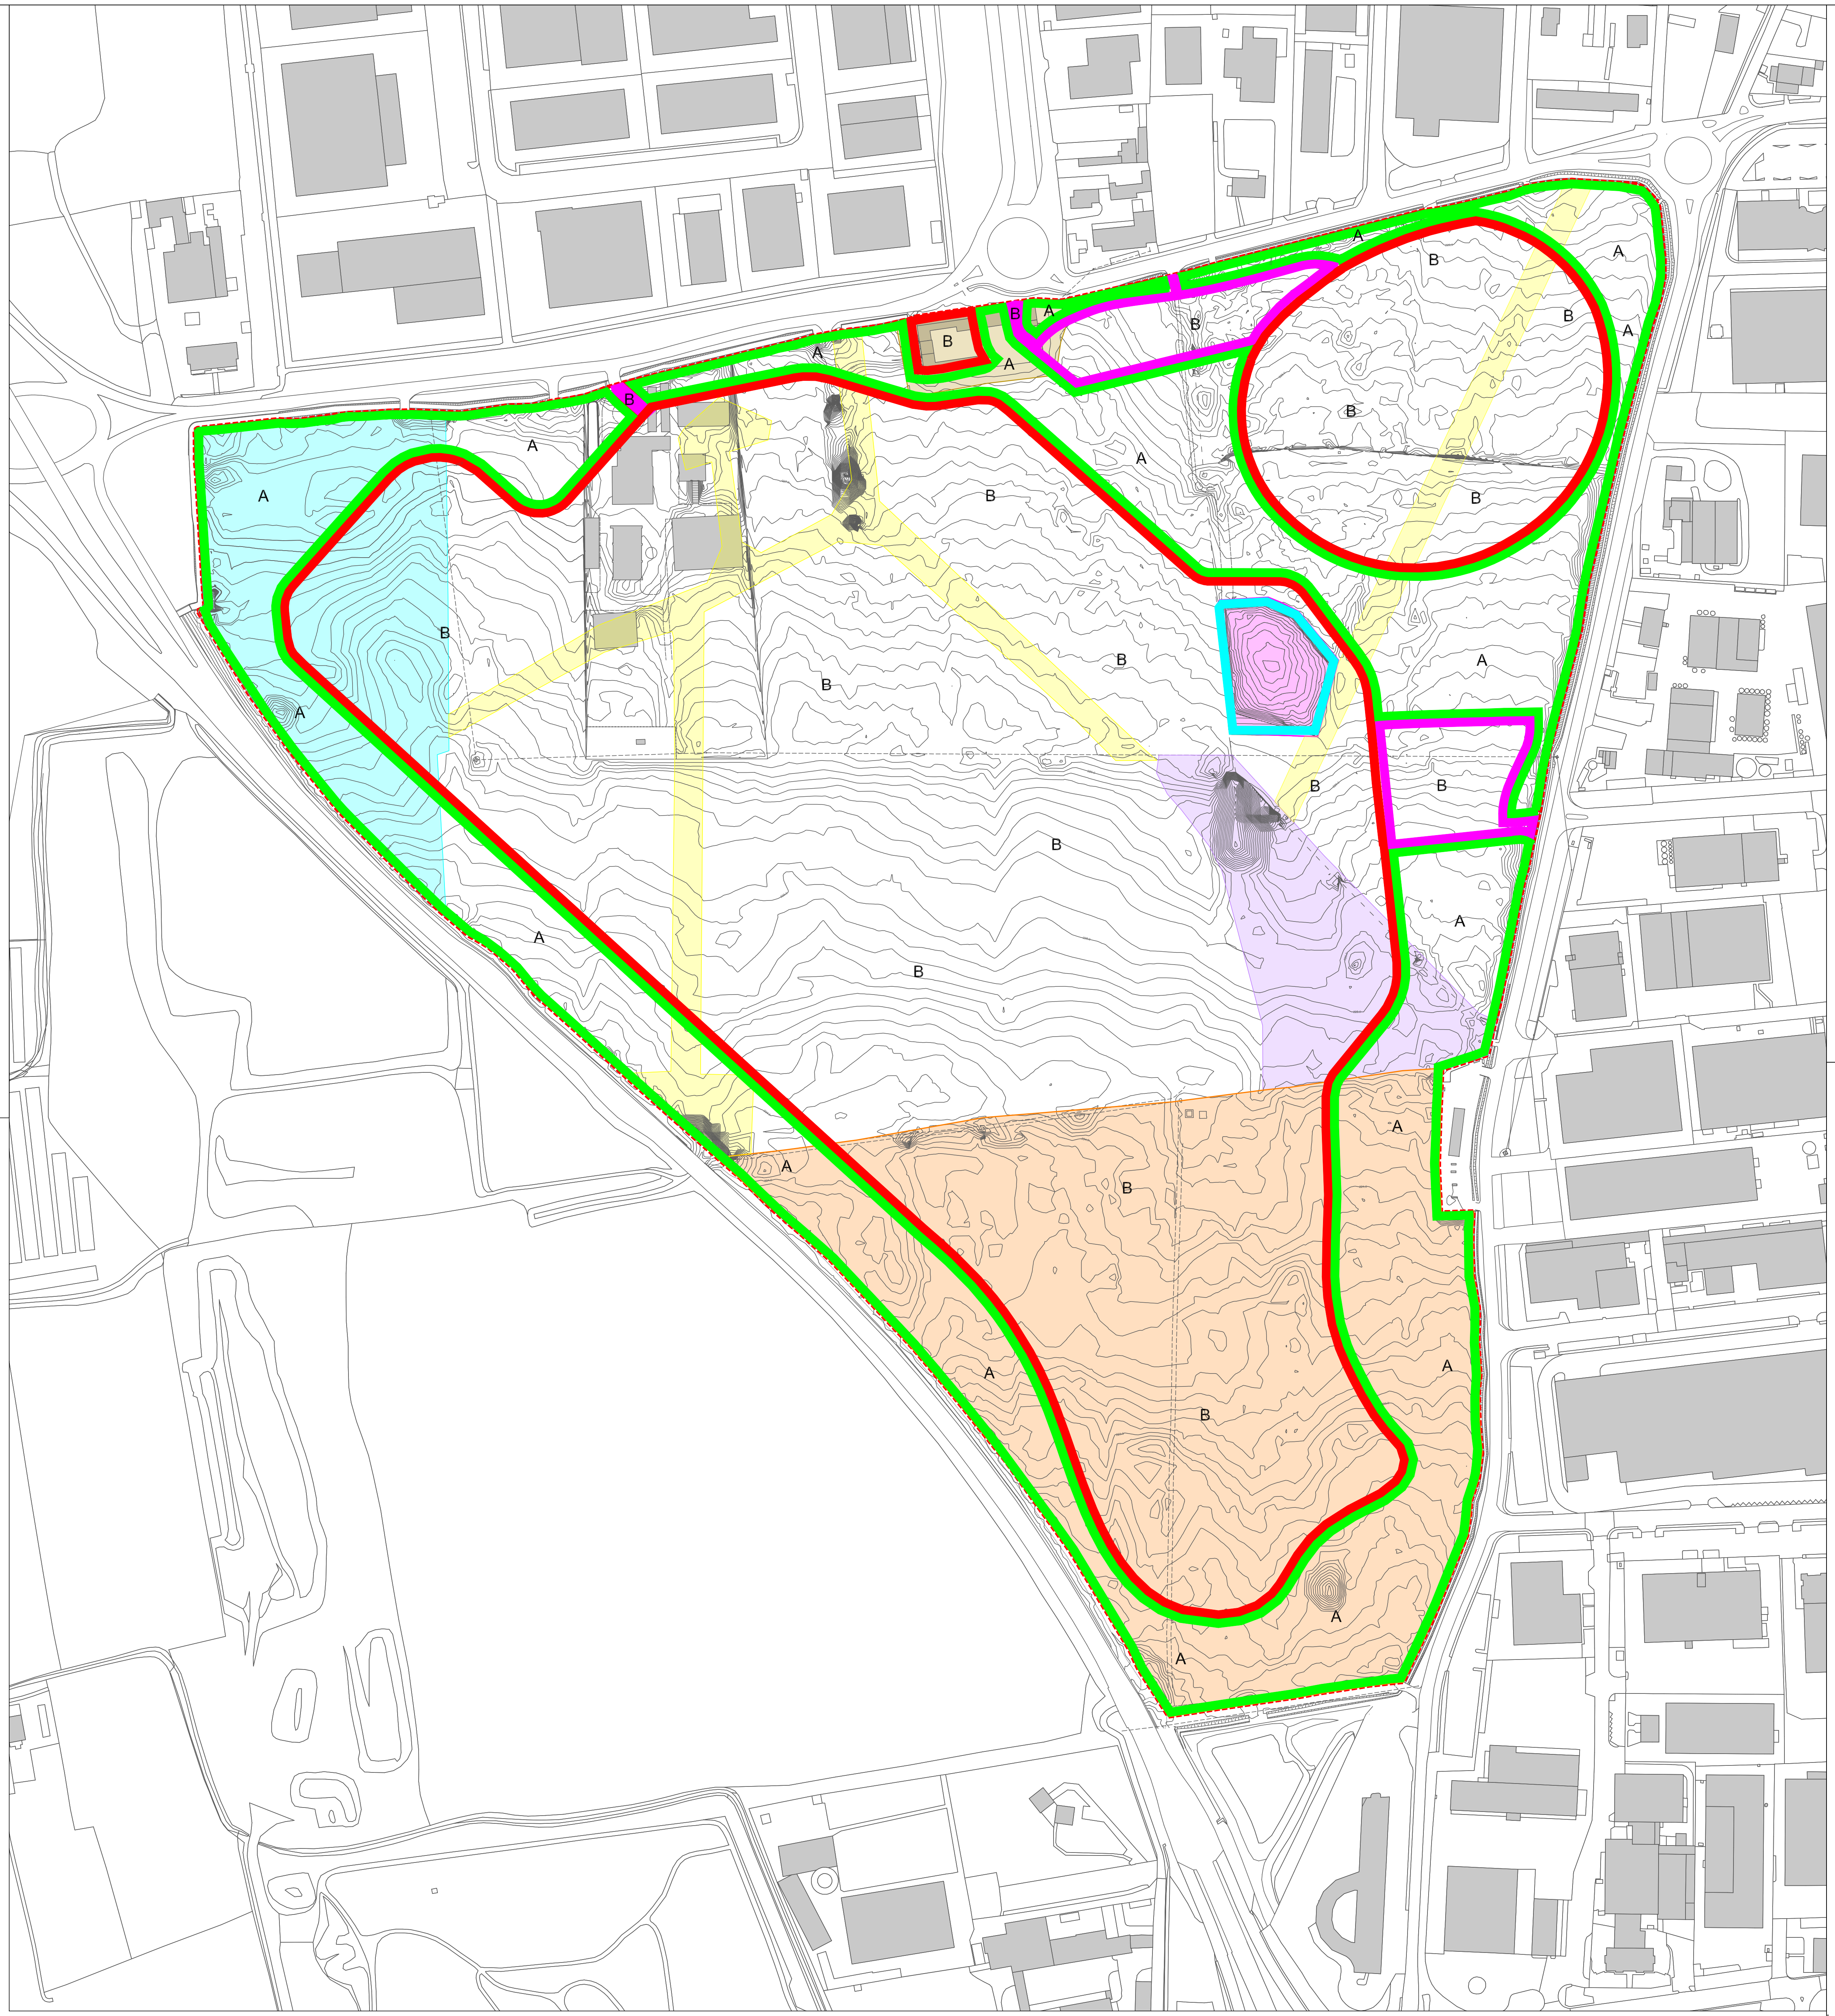

STATO DI FATTO: PLANIMETRIA GENERALE AREA DI INTERVENTO

LEGENDA

- ▭ Perimetro Ambito

🟩 A — Aree destinate a parco urbano territoriale con fruizione ludico sportiva
Queste aree devono essere recuperate rispettando i limiti di Tabella A

🟪 B — Aree destinate ad infrastrutture pubbliche (parcheggi e viabilità).
Queste aree possono essere recuperate rispettando la tabella B

🟥 B — Aree destinate ad attività produttive e terziario direzionale.
Queste aree possono essere recuperate rispettando la tabella B

🟦 Aree ex discarica Cucco.
Queste aree non possono essere utilizzate e vanno preservate nello stato di fatto

ACCORDO DI PROGRAMMA

RIGENERAZIONE URBANA E TERRITORIALE DELL'EX AMBITO ESTRATTIVO DEL PADERGNONE

NUOVO POLO TECNOLOGICO DI INTERESSE SOVRALOCALE

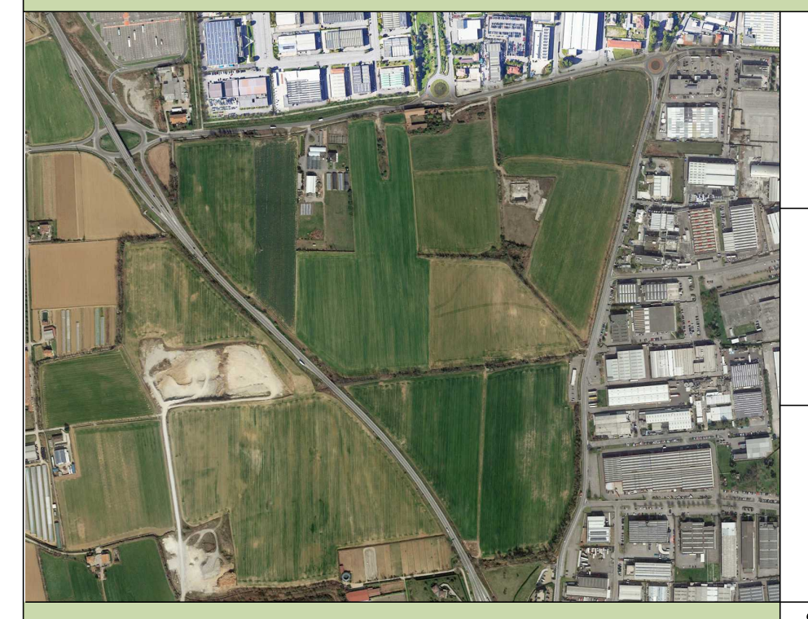

PROVINCIA DI BERGAMO
Via Torquato Tasso 8
24121 Bergamo
PEC protocollo@pec.provincia.bergamo.it
Tel 035387111

COMUNE DI ZANICA
Via Roma 35
24050 Zanica
PEC protocollo@pec.comune.zanica.bg.it
Tel 0354245811

PROMOTORE
Real Estate SPV Project 2415 S.r.l.
Corso Vittorio Emanuele II No. 24/28
20122 – Milano (Italia)
PEC realestatespvproject2415@legalmail.it
Tel +39 02 7788051 -

D - PIANIFICAZIONE ATTUATIVA

SCALA 1:2000	DATA LUGLIO 2026	
TITOLO TAVOLA: **STATO DI FATTO: CRITICITA' GEOLOGICHE E CONTAMINAZIONI BONIFICHE AMBIENTALI PREVISTE**	NUMERO TAVOLA **D2**	AGGIORN. AGGIORN. AGGIORN.

N

TAVOLO TECNICO ISTITUZIONALE

COMUNE DI ZANICA:
UFFICIO URBANISTICA EDILIZIA PRIVATA E SUE
Dirigente
Dott. arch. Gianluca Della Mea
gianluca.dellamea@comune.zanica.bg.it
tel. 035 4245811 int 3

PROGETTISTI E CONSULENTI

PROGETTO URBANISTICO E COORDINAMENTO GENERALE
Marcello Fiorina - ingegnere
Elisabetta Nani - ingegnere
Studio associato di architettura urbanistica ed ingegneria
Sede in via pignolo 5, Bergamo tel 035-218094 - 035-270308
www.studiofiorina.com - indirizzo email: info@studiofiorina.com

PAESAGGIO AMBIENTE E NATURA
STUDIO GERUNDO
Studio Gerundo
Arch. Paolo Pellicciol
Ing. Susanna Quirico
Dott. Agr. Alberto Massa Saluzzo
Via Cagnola 25 – Treviglio
Tel 3475331955 e-mail: info@studiogerundo.it

RKD
Kevin Maguire
Derek Meenan
The Eight Building
Dublin - Ireland - D08 T2TX
Tel +353 1 668 1055 e-mail: mail@rkd.ie
https://www.rkd.ie

BEAST Design Studios GmbH
Gustavo Espigado
Kölner Str. 1
Eschborn - Germany - 65760
Tel +49 (0) 6196 7700 410
e-mail: g.espigado@beastdesignstudios.com
www.beastdesignstudios.com

ETS Engineering and Technical Services SpA
Donato Romano
Via Angelo Mazzi, 32
Villa d'Almè - Bergamo - 24018
Tel +39 035 6313111 e-mail: info@etseng.it
https://www.etseng.it/

TRASPORTI, AMBIENTE, INVARIANZA IDRAULICA
TE.A. CONSULTING SRL
ING. MASSIMO MOI
MI Via G.B. Grassi 15 - 20157 Milano (MI)
T 02 21711067
BG Via Don A. Mazzucotelli 6 - 24020 Gorle (BG)
T 035 321360
www.territorioambiente.com

VALUTAZIONE AMBIENTALE STRATEGICA
TE.A. CONSULTING SRL
ING. MASSIMO MOI
MI Via G.B. Grassi 15 - 20157 Milano (MI)
T 02 21711067
BG Via Don A. Mazzucotelli 6 - 24020 Gorle (BG)
T 035 321360
www.territorioambiente.com

H&MV Engineering
Paul O'Helleran, Fabio Sbacches
Hamilton House Block 2
Castletroy - Ireland - V94 YHD6
Tel +35 36 135 7496 e-mail: info@hmvengineering.com
https://www.hmvengineering.com/