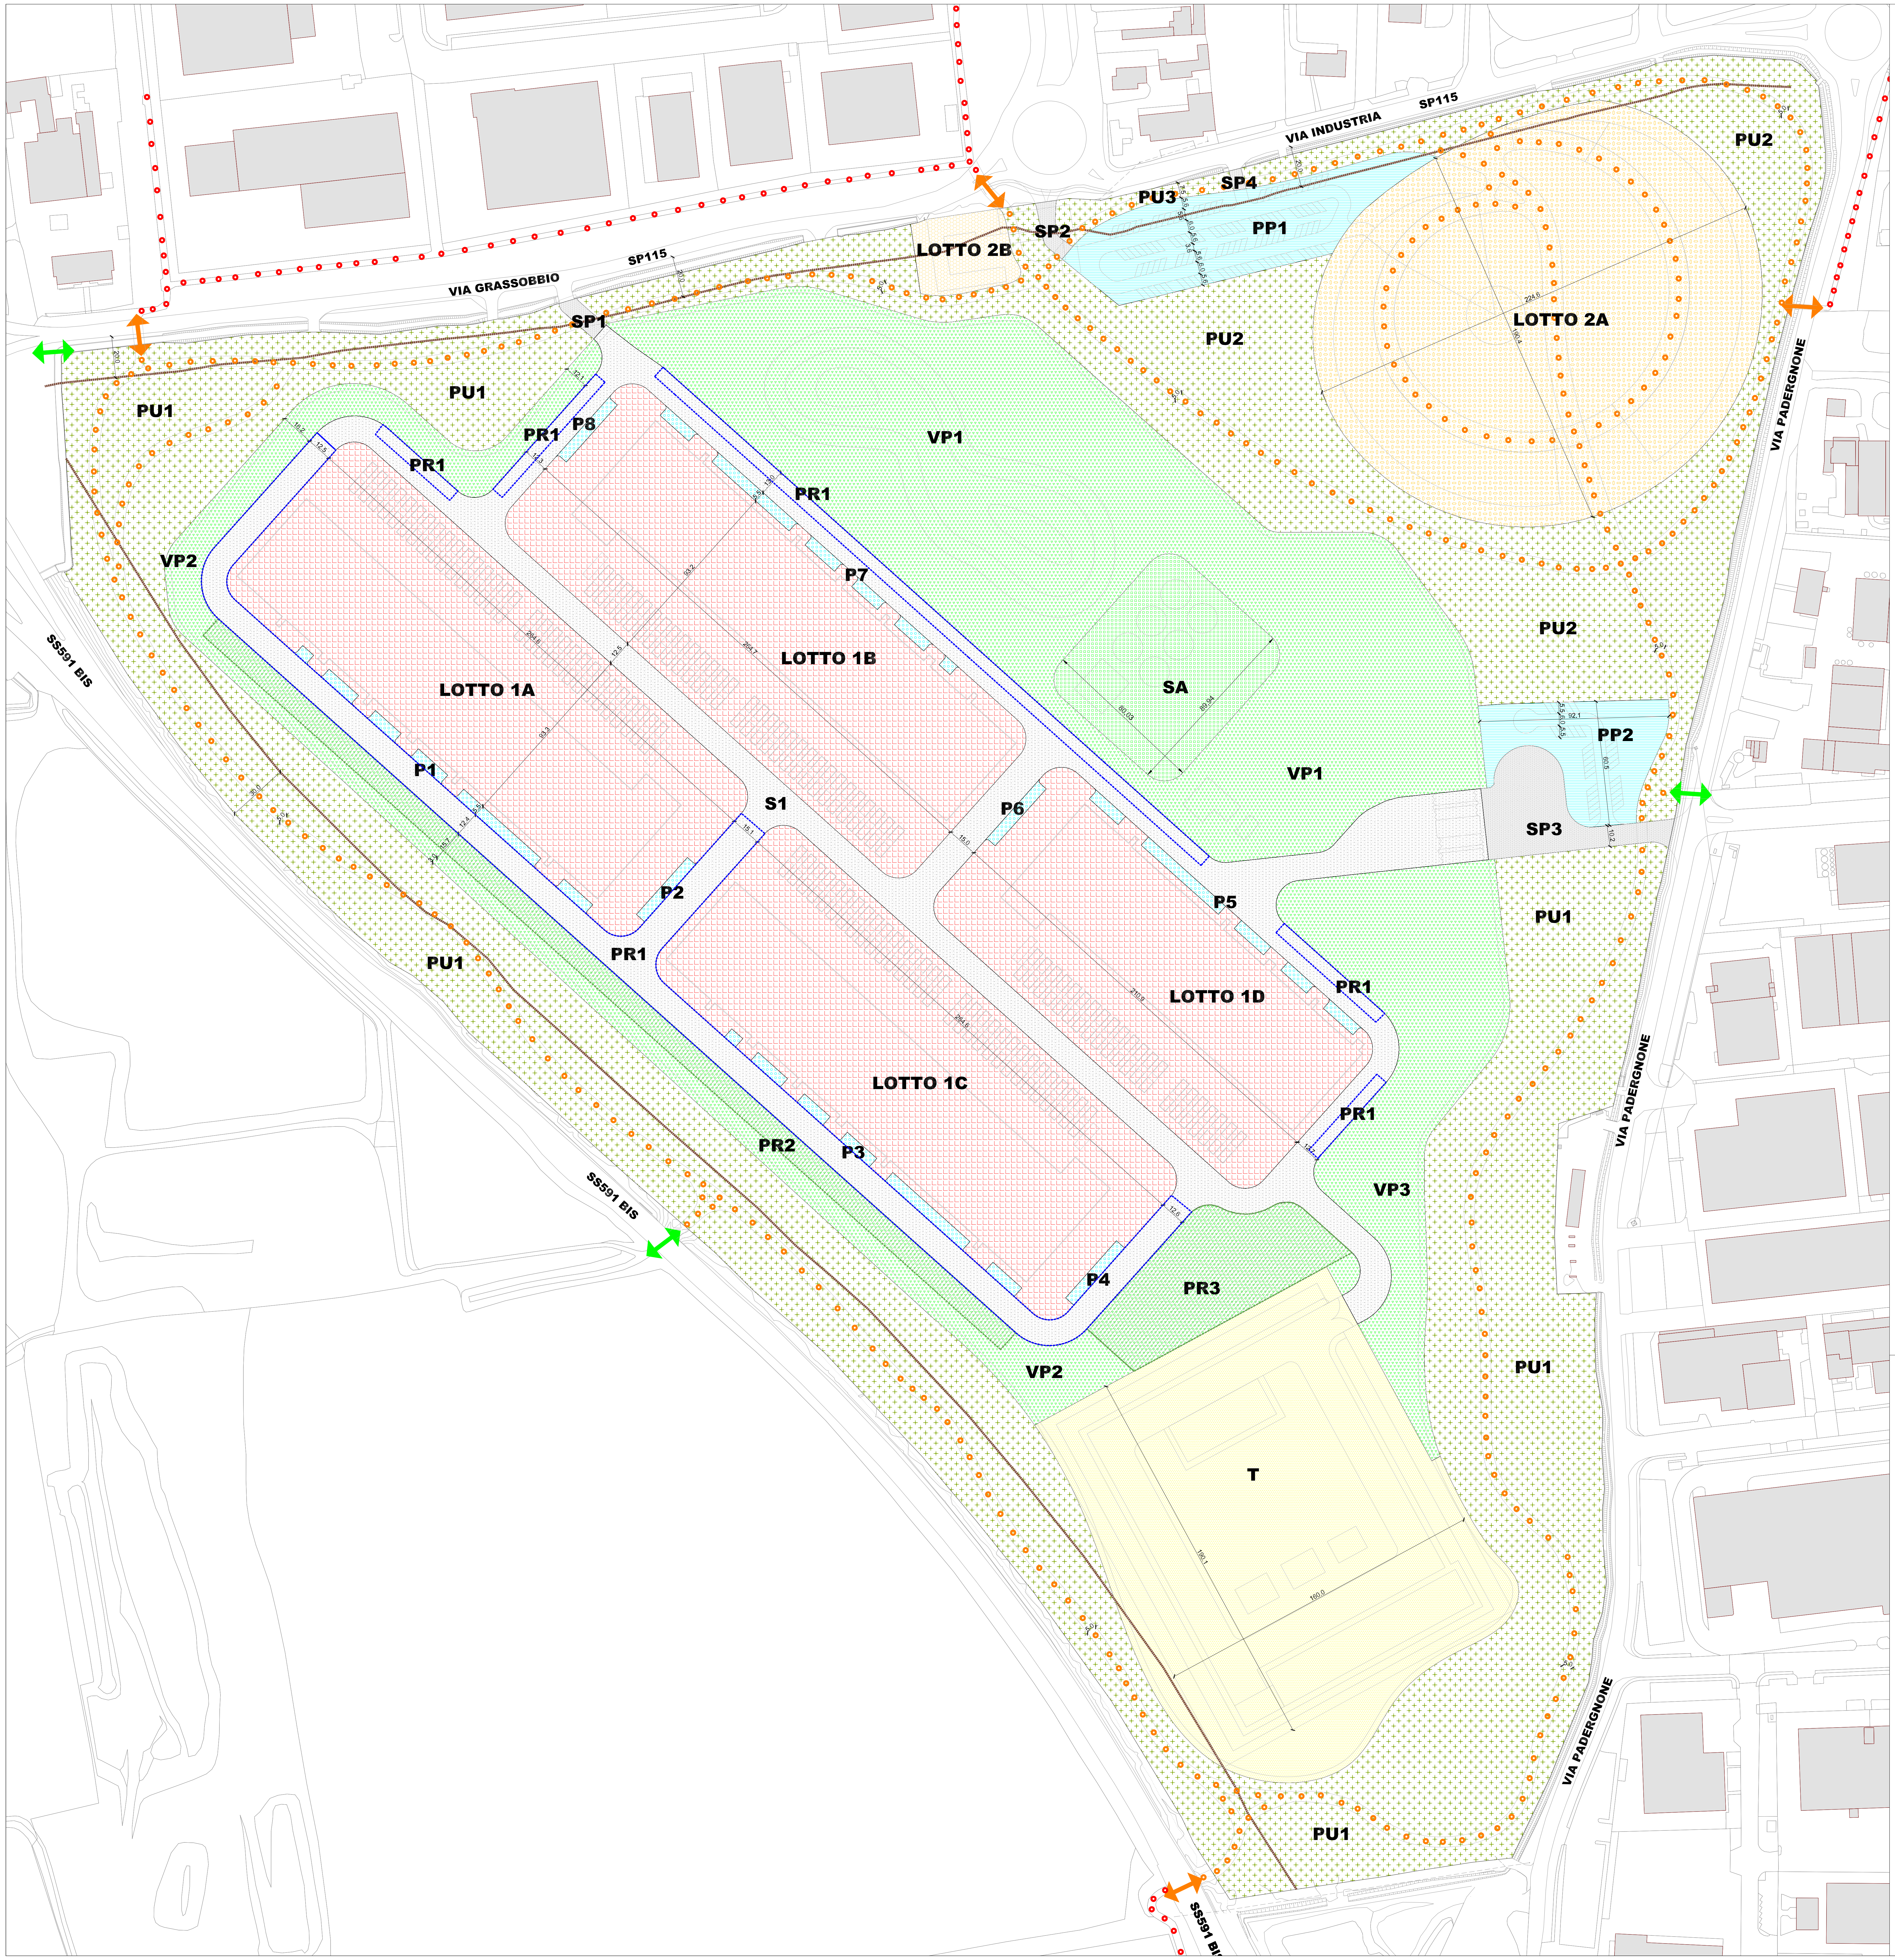

RIQUALIFICAZIONE AREE ACCORDO DI PROGRAMMA

ZONA URBANISTICA	(mq)	SC (mq)	SL (mq)	permeabile	altezza
LOTTO 1- DATACENTER					
Area edificabile Datacenter (1A-1B-1C-1D)	95.263	46.509	93.018	no	25 m
Parcheggi privati (P1- P8)	9.592			semi	
Aree verdi private (VP1-VP2-VP3)	82.303			si	
Area depositi esterni acqua di processo (SA)	7.080			semi	
Viabilità privata interna (S1)	27.494			no	
Stazione Terna (T)	34.188			semi	
Totale lotto 1 -SF-	**255.920**	**46.509**	**93.018**		
LOTTO 2A - TECH HUB					
Area edificabile Tech hub (2A)	34.575	11.400	40.000	no	18 m
Totale lotto 2A -SF-	**34.575**	**11.400**	**40.000**		
LOTTO 2B - CASCINA CUCCO					
Edificio cascina Cucco (2B)	1.753	750	1.500	no	esist
Totale lotto 2B -SF-	**1.753**	**750**	**1.500**		
AREE PUBBLICHE					
Parco urbano territoriale (PU1-PU2-PU3)	132.743			si	
Parcheggio pubblico in superficie (PP1-PP2)	9.696			no	
Viabilità di accesso pubblica (SP1-SP2-SP3-SP4)	2.950			no	
Totale aree pubbliche o asservite uso pubblico	**145.389**				
TOTALE SUPERFICIE GENERALE - ST -	**437.637**	**58.659**	**134.518**		
			<		
PREVISIONE PGT VIGENTE	**438.595**	**-**	**152.500**		

ALTEZZA MASSIMA DA PIANIFICAZIONE VINCOLI AEREOPORTUALI ENAC

L'ambito è interessato dalla presenza di vincolo aeroportuale e, in particolare, dalla superficie orizzontale interna che pone quale limite altimetrico degli edifici l'altezza di 274,95m s.l.m., altezza che consente, in ogni caso, un franco libero medio di prima approssimazione di oltre 45m. (da quota terreno circa 228/229 metri s.l.m.)

SUPERFICI ACCESSORIE AREE TECNICHE

ZONA URBANISTICA	(mq)	SA (mq)	altezza
STAZIONE TERNA (T)	34.188	7.000	18 m
AREA DEPOSITI ESTERNI ACQUE DI PROCESSO (SA)	7.080	2.600	18 m

VERIFICA DOTAZIONE COMPLESSIVA STANDARD URBANISTICI

		Dotazione pubblica attesa	
	mq	%	mq.
Superficie lorda produttiva	93.018	20% SL	18.604
Superficie lorda terziario direzionale ricettiva commerciale	40.000	100% SL	40.000
Superficie lorda terziario direzionale ricettiva commerciale Cascina Cucco	1.500	100% SL	1.500
Dotazione aggiuntiva piste ciclabili (su tutta la SL)	134.518	9mq/50mqSL	24.213
Totale			**84.317**
di cui a parcheggio			30.052
di cui a parco urbano			30.052
di cui al servizio ciclabile			24.213

	Dotazione pubblica garantita
	mq.
Parco urbano territoriale (PU1-PU2-PU3) comprensivo di 24.213 mq di aree al servizio delle piste ciclabili	132.743
Parcheggio pubblico in superficie (PP1-PP2)	9.696
Totale	**142.439**

	Attesa mq		Garantita mq
Totale dotazione pubblica	**84.317**	<	**142.439**

VERIFICA DOTAZIONE AREE PER LA SOSTA PUBBLICA

	ST (mq)	Dotazione pubblica attesa		realizzata
	mq	%	mq.	mq.
Superficie lorda produttiva	93.018	10% SL	9.302	0
Superficie lorda terziario direzionale ricettiva commerciale	41.500	50% SL	20.750	9.696
Totale	134.518		30.052	9.696

Nb. 1 - DATACENTER - In ragione della specificità tecnologica e dei requisiti di sicurezza del Data Center, che impongono il massimo controllo degli accessi, non sono previsti parcheggi di libero accesso pubblico. La dotazione di sosta necessaria al funzionamento della struttura è integralmente garantita all'interno dell'area pertinenziale. Le aree a parcheggio derivanti dagli obblighi di standard sono pertanto reperite mediante la cessione del Parco Urbano Territoriale che viene incrementato di 9.302 mq., assicurando il rispetto della dotazione complessiva dovuta e orientando la cessione verso una funzione pubblica più coerente con gli obiettivi di mitigazione e qualificazione territoriale.

Nb. 2 - TECH HUB e CASCINA CUCCO - A seguito degli approfondimenti trasportistici svolti, e con la finalità di contenere al massimo gli impatti al suolo, si prevede la cessione di aree a parcheggio pubblico per una superficie pari a 9.696 mq. La dotazione di sosta necessaria al funzionamento del compendio immobiliare sarà garantita mediante parcheggi pertinenziali privati realizzati in struttura. Di conseguenza e sulla base di studi tecnici di viabilità e della relativa relazione trasportistica, le aree a parcheggio derivanti dagli obblighi di standard e non reperite a raso saranno compensate mediante la cessione aggiuntiva di aree destinate a Parco Urbano Territoriale, che risulta pertanto incrementato di 11.054 mq, assicurando il rispetto della dotazione complessiva dovuta a standard ma orientando la fruizione pubblica verso una soluzione più coerente sotto il profilo ambientale e paesaggistico.

Nb. 3 - PARCO URBANO E PISTE CICLABILI - Il progetto di Piano garantisce all'interno della vasta area di Parco urbano Territoriale anche gli spazi funzionali al sistema delle reti ciclabili dimensionate in misura non inferiore ai 24.213 mq. previsti dalle norme del PdS. Al netto di tali superfici e delle superfici a parcheggio che non vengono realizzate e compensate a Parco (20.356 mq) il Parco urbano consta di 88.174 mq. ben superiore ai 30.052 previsti dal PGT.

VERIFICA DOTAZIONE SOSTA PRIVATA (ex L. 122/89)

ST (mq) — **Il volume è determinato applicando l'altezza virtuale standard di 3 metri**

		Dotazione sosta attesa 1mq ogni 10mc			realizzata/ realizzabi
	mq	mc	1/10 mq		mq.
Superficie lorda produttiva **DATACENTER**	93.018	279.054	27.905		
Parcheggi privati (P1-P2-P3-P4-P5-P6-P7-P8) (fabbisogno reale/operatività a regime)					3.640
Altre superfici eventualmente reperibili					
Parcheggi di riserva privati eventualmente reperibili su superfici già pavimentate interne alla proprietà (PR1)					14.049
Parcheggi di riserva privati eventualmente reperibili su superfici permeabili e mantenute permeabili (PR2/3)					10.853
Totale			27.905	<	28.542

		Dotazione sosta attesa 1mq ogni 10mc			realizzata
	mq	mc	1/10 mq		mq.
Superficie lorda **TECH HUB** e Cascina Cucco	41.500	124.500	12.450		
Parcheggi da realizzare in struttura					12.450
Totale			12.450	=	12.450

La dotazione di parcheggi privati, disciplinata in via generale dalla legge Tognoli (L. 122/1989), si basa su un criterio concepito per funzioni ad alta densità di presenze che, applicato a un data center, caratterizzato da un numero di addetti più contenuto, determina un fabbisogno teorico ampiamente superiore alle effettive necessità dell'insediamento. Coerentemente, il progetto individua 3.640 mq di parcheggi privati, dimensionati sulla reale operatività a regime degli edifici del data center. Qualora si rendesse necessario integrare la dotazione di parcheggi fino agli ulteriori 24.265 mq teoricamente richiesti dalla L. 122/1989, le superfici richieste potrebbero essere reperite mediante la riconversione di circa 14.049 mq di aree pavimentate destinate alle connessioni interne e, per la quota residua, attraverso parcheggi permeabili lungo le fasce verdi adiacenti alla viabilità.
Il progetto risulta pertanto in grado di garantire, ove necessario, una dotazione di sosta anche superiore ai minimi normativi, evitando tuttavia di realizzare fin da subito infrastrutture non giustificate dalle effettive esigenze dell'insediamento. Tale impostazione trova conferma nella recente normativa regionale, che per i data center consente una riduzione fino al 75% dei parcheggi privati determinati ai sensi della legge Tognoli, riconoscendo la minore domanda di sosta propria di tali funzioni.

PERCORSI CICLABILI

	km
Percorso ciclabile esterno	2,8
Percorso ciclabile interno	2,5
Varianti	1,4
Totale percorsi ciclabili	4,2

VERIFICA DOTAZIONE SUPERFICIE PERMEABILI

	ST (mq)				Permeabile
		Permeabile da regolamento edilizio			
Superficie territoriale generale dell'intervento	437.637	15%	65.646		
		Permeabile da PGT			Garantita
Superficie territoriale generale dell'intervento	437.637	30%	**131.291**	<	**215.046**
Aree verdi private (VP1-VP2-VP3)					82.303
Parco urbano territoriale (PU1-PU2-PU3)					132.743
Totale aree permeabili garantite					**215.046**
Totale aree permeabili garantite in % sulla ST		**30,0%**	<		**49,1%**

NB. Oltre alle aree permeabili indicate, all'interno della zona Tech Hub potranno essere realizzate ulteriori aree permeabili che andranno a migliorare ulteriormente il parametro complessivo

VERIFICA AREE LIBERE PER RIDUZIONE CONSUMO DI SUOLO

	mq.
Superficie di suolo libero minima da garantire nel Piano (da scheda PGT)	**120.000**
	<
Superficie suolo libero garantita (Parco urbano territoriale PU1-PU2-PU3)	**132.743**

LEGENDA

🟥	Perimetro Ambito
▦	Lotti edificabili Data Center (1)
▤	PP - Parcheggi pubblici in superficie
▨	P - Parcheggi privati in superficie
▭	PR1 - Parcheggi di riserva privati reperibili su aree già pavimentate
▨	PR2 - Parcheggi di riserva privati reperibili su aree permeabili e mantenute permeabili
▨	SP - Viabilità pubblica
▨	S - Viabilità privata
―	Fasce di rispetto strade
● ● ● ●	Percorso ciclopedonale di progetto
● ● ● ●	Percorso ciclopedonale esistente non oggetto di intervento
═	Recinzione: la linea di difesa del Datacenter è costituita da una doppia recinzione con spazio interno di 3 metri
▨	Lotto edificabile Tech Hub (2A)
▨	Lotto terziario Cascina Cucco (2B)
▨	T - Stazione elettrica
▦	SA - Aree di stoccaggio acqua
▨	VP - Aree a verde di pertinenza Data Center
▨	PU - Parco urbano territoriale
↔	Collegamenti a ciclabili a percorsi esterni esistenti
↔	Connessioni ciclabili a possibili sviluppi futuri della rete esterna

ACCORDO DI PROGRAMMA
RIGENERAZIONE URBANA E TERRITORIALE DELL'EX AMBITO ESTRATTIVO DEL PADERGNONE
NUOVO POLO TECNOLOGICO DI INTERESSE SOVRALOCALE

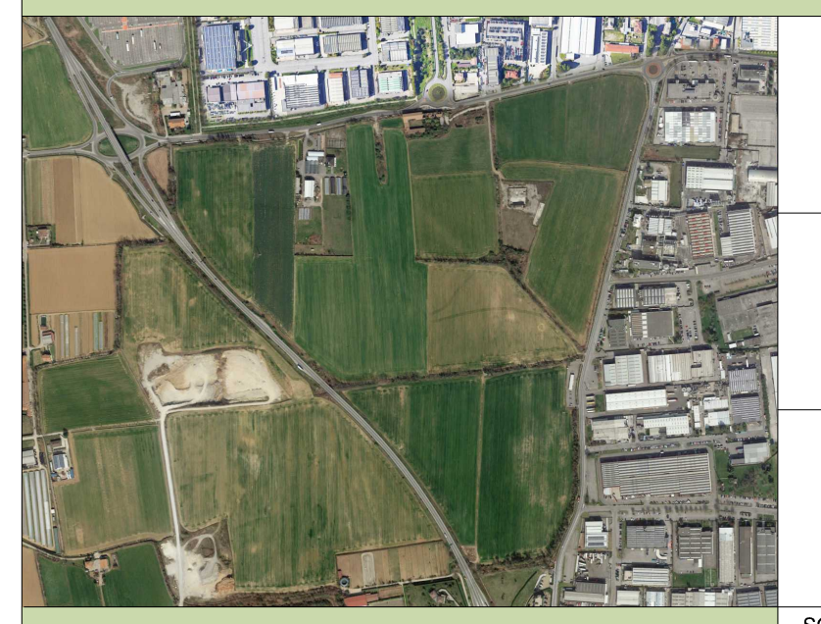

PROVINCIA DI BERGAMO
Via Torquato Tasso 8
24121 Bergamo
PEC protocollo@pec.provincia.bergamo.it
Tel 035387111

COMUNE DI ZANICA
Via Roma 35
24050 Zanica
PEC protocollo@pec.comune.zanica.bg.it
Tel 0354245811

PROMOTORE
Real Estate SPV Project 2415 S.r.l.
Corso Vittorio Emanuele II No. 24/28
20122 – Milano (Italia)
PEC realestatespvproject2415@legalmail.it
Tel +39 02 7788051 -

D - PIANIFICAZIONE ATTUATIVA

SCALA 1:1000
DATA SETTEMBRE 2026
TITOLO TAVOLA **CARTA DELLE REGOLE URBANISTICHE**
NUMERO TAVOLA **D4**
AGGIORN.
AGGIORN.
AGGIORN.
N

TAVOLO TECNICO ISTITUZIONALE

COMUNE DI ZANICA:
UFFICIO URBANISTICA EDILIZIA PRIVATA E SUE
Dirigente
Dott. arch. Gianluca Della Mea
gianluca.dellamea@comune.zanica.bg.it
tel. 035 4245811 int 3

PROGETTISTI E CONSULENTI

PROGETTO URBANISTICO E COORDINAMENTO GENERALE
Marcello Fiorina - ingegnere
Elisabetta Nani - ingegnere
Studio associato di architettura urbanistica ed ingegneria
Sede in via pignolo 5, Bergamo tel 035-218094 - 035-270308
www.studiofiorina.com - indirizzo email: info@studiofiorina.com

PAESAGGIO AMBIENTE E NATURA
Studio Gerundo
Arch. Paolo Pelliccioli
Ing. Susanna Quirico
Dott. Agr. Alberto Massa Saluzzo
Via Cagnola 25 – Treviglio
Tel 3475331955 e-mail: info@studiogerundo.it

TECH CONCEPT AND ARCHITECTURAL
RKD
Kevin Maguire
Derek Meenan
The Eight Building
Dublin - Ireland - D08 T2TX
Tel +353 1 668 1055 e-mail: mail@rkd.ie
https://www.rkd.ie

TECH CONCEPT AND ARCHITECTURAL
BEAST Design Studios GmbH
Gustavo Espigado
Kölner Str. 1
Eschborn - Germany - 65760
Tel +49 (0) 6196 7700 410
e-mail: g.espigado@beastdesignstudios.com
www.beastdesignstudios.com

ENGINEERING AND INFRASTRUCTURE
ETS Engineering and Technical Services SpA
Donato Romano
Via Angelo Mazzi, 32
Villa d'Almè - Bergamo - 24018
Tel +39 035 6313111 e-mail: info@etseng.it
https://www.etseng.it/

TRASPORTI, AMBIENTE, INVARIANZA IDRAULICA
TE.A. CONSULTING SRL
ING. MASSIMO MOI
MI Via G.B. Grassi 15 - 20157 Milano (MI)
T 02 21711067
BG Via Don A. Mazzucotelli 6 - 24020 Gorle (BG)
T 035 321360
www.territorioambiente.com

VALUTAZIONE AMBIENTALE STRATEGICA
TE.A. CONSULTING SRL
ING. MASSIMO MOI
MI Via G.B. Grassi 15 - 20157 Milano (MI)
T 02 21711067
BG Via Don A. Mazzucotelli 6 - 24020 Gorle (BG)
T 035 321360
www.territorioambiente.com

POWER AND INFRASTRUCTURE
H&MV Engineering
Paul O'Helleran, Fabio Sbacches
Hamilton House Block 2
Castletroy - Ireland - V94 YHD6
Tel +35 36 135 7496 e-mail: info@hmvengineering.com
https://www.hmvengineering.com/