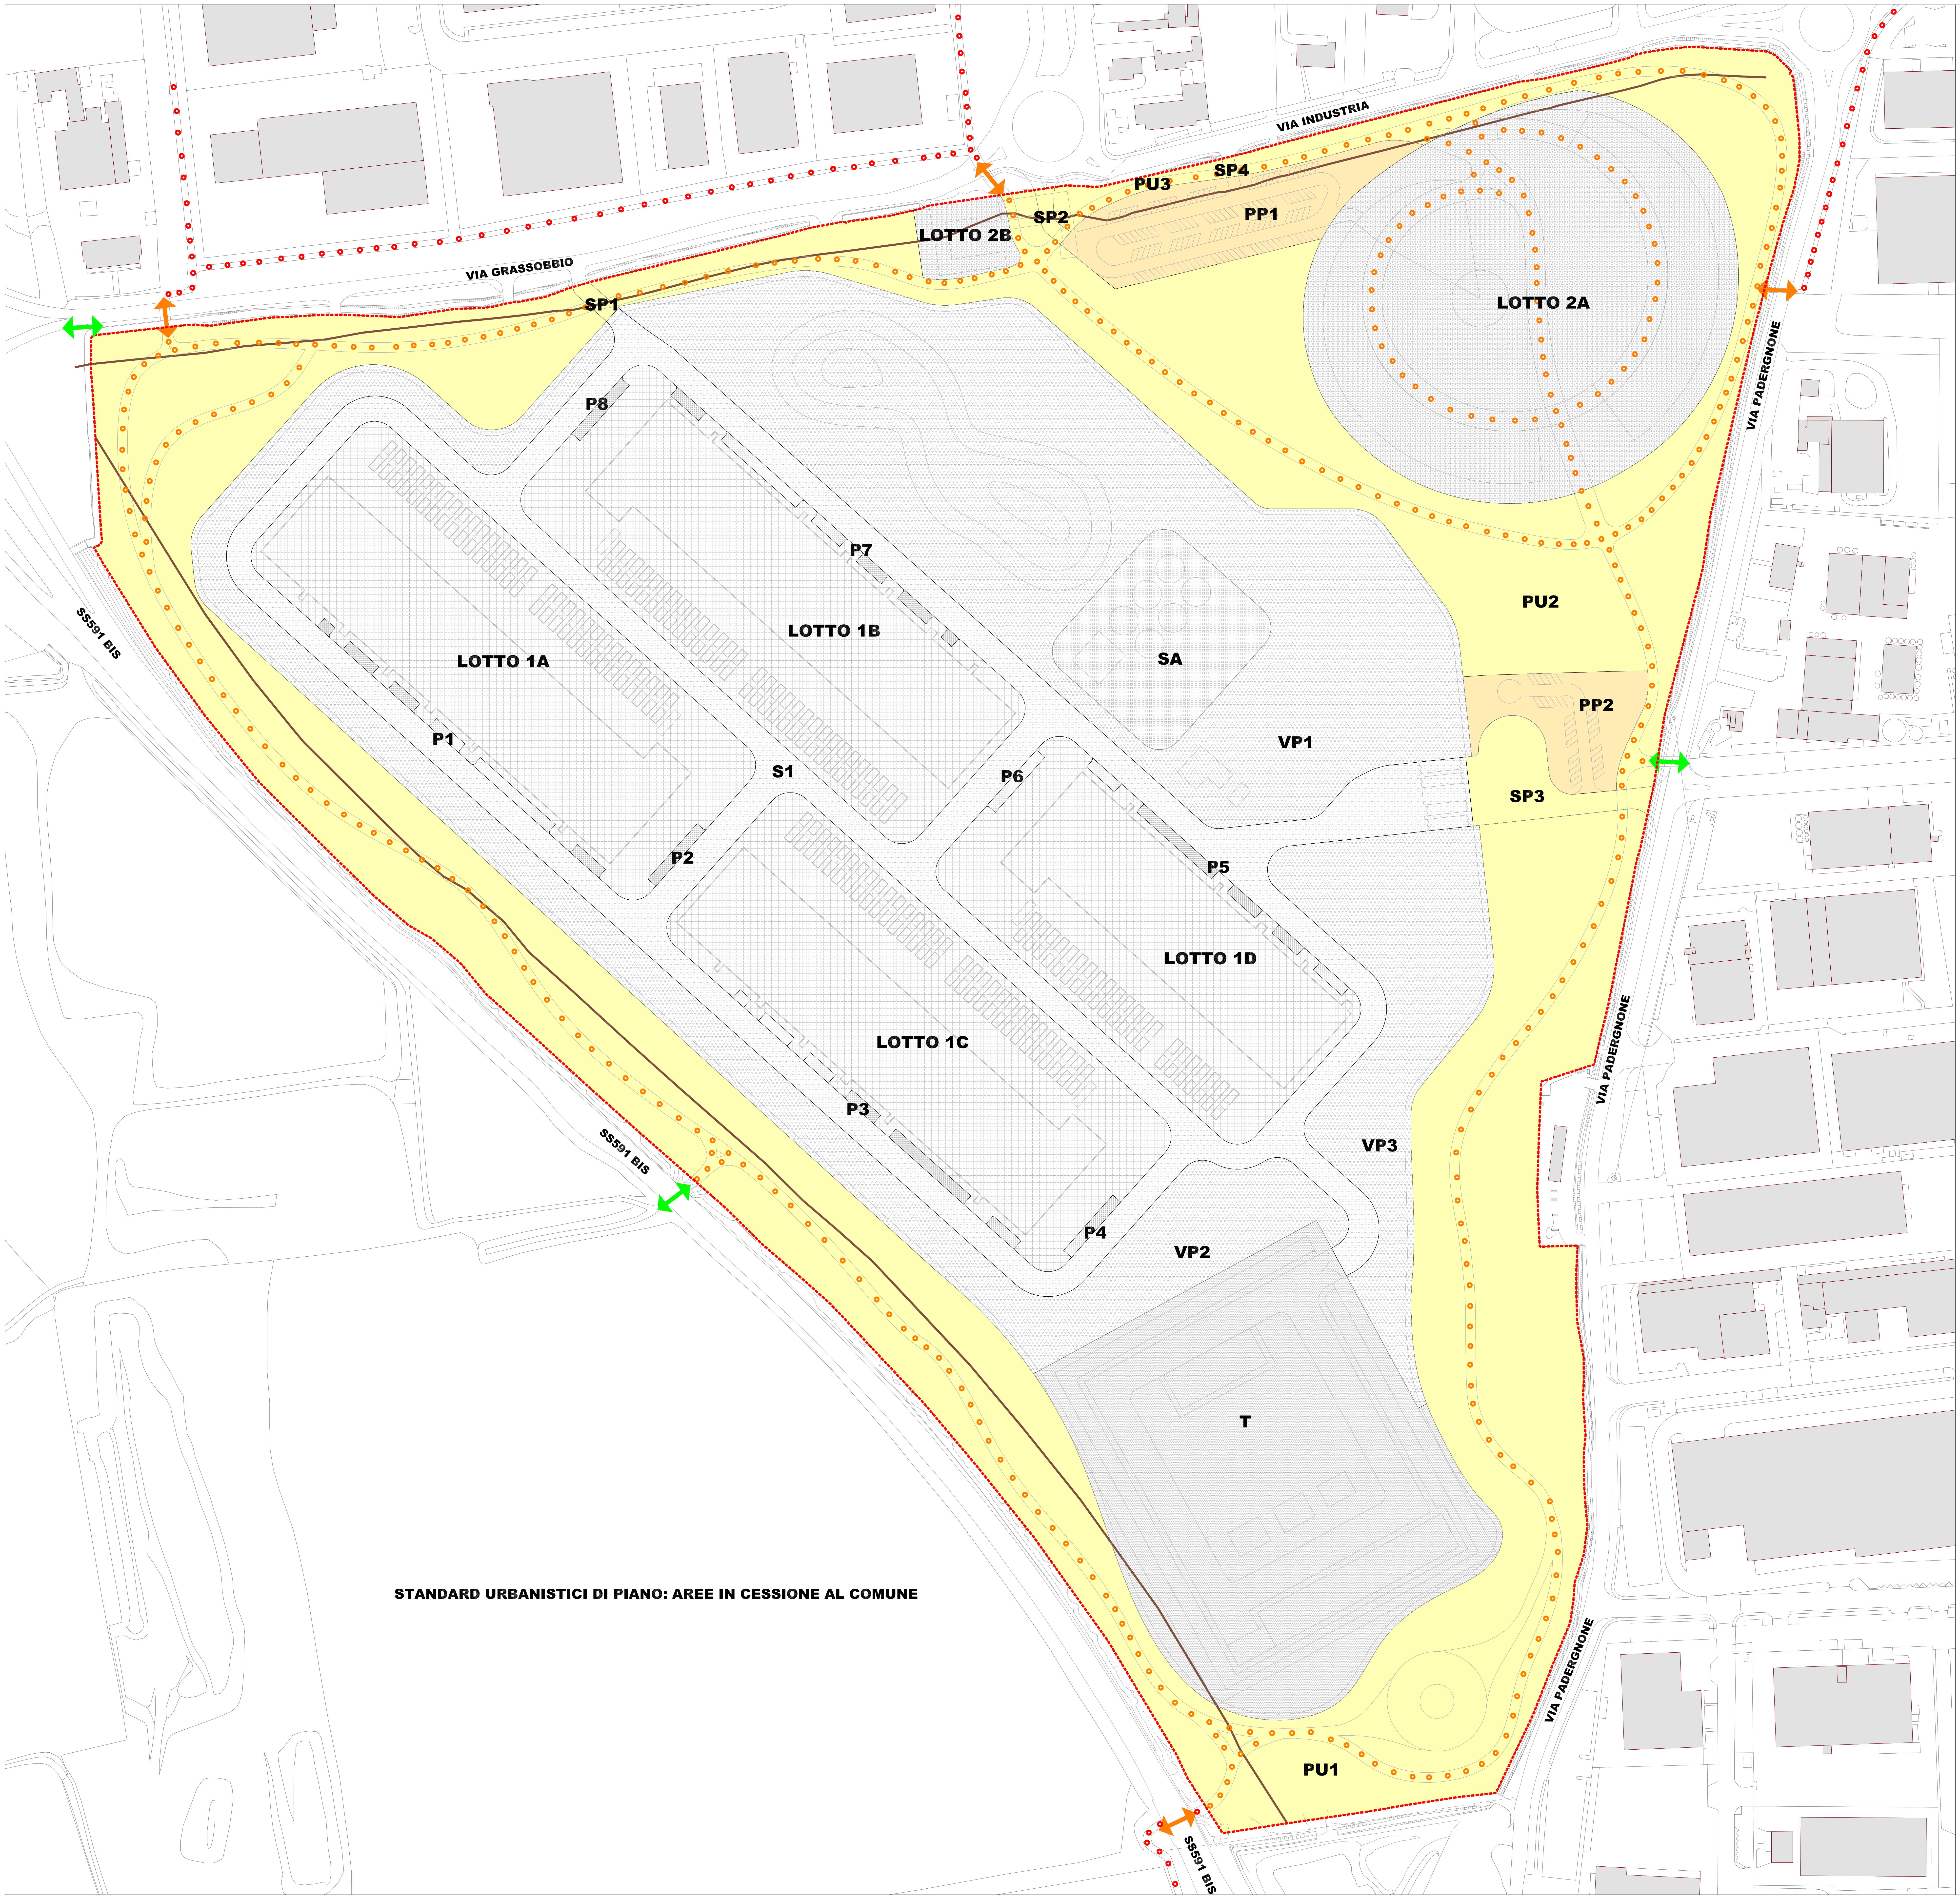

STANDARD URBANISTICI DI PIANO: AREE IN CESSIONE AL COMUNE

VERIFICA DOTAZIONE COMPLESSIVA STANDARD URBANISTICI

		Dotazione pubblica attesa	
	mq	%	mq.
Superficie lorda produttiva	93.018	20% SL	18.604
Superficie lorda terziario direzionale commerciale	40.000	100% SL	40.000
Superficie terziaria Cascina Cucco	1.500	100% SL	1.500
Dotazione aggiuntiva piste ciclabili (su tutta la SL)	134.518	9mq/50mqSL	24.213
Totale			**84.317**

	Dotazione pubblica garantita
	mq.
Parco urbano territoriale (PU1-PU2-PU3)	132.743
Parcheggio pubblico in superficie (PP1-PP2)	9.696
Totale	**142.439**

	Attesa mq		Garantita mq
Totale dotazione pubblica	**84.317**	<	**142.439**

VERIFICA DOTAZIONE AREE PER LA SOSTA PUBBLICA **ST (mq)**

		Dotazione pubblica attesa		realizzata
	mq	%	mq.	mq.
Superficie lorda produttiva	93.018	10% SL	9.302	0
Superficie lorda terziario direzionale commerciale	41.500	50% SL	20.750	9.696
Totale	134.518		30.052	9.696

Nb. 1 - DATACENTER - In ragione della specificità tecnologica e dei requisiti di sicurezza del Data Center, che impongono il massimo controllo degli accessi, non sono previsti parcheggi di libero accesso pubblico. La dotazione di sosta necessaria al funzionamento della struttura è integralmente garantita all'interno dell'area pertinenziale. Le aree a parcheggio derivanti dagli obblighi di standard sono pertanto reperite mediante la cessione del Parco Urbano Territoriale che viene incrementato di 9.302 mq., assicurando il rispetto della dotazione complessiva dovuta e orientando la cessione verso una funzione pubblica più coerente con gli obiettivi di mitigazione e qualificazione territoriale.

Nb. 2 - TECH HUB e CASCINA CUCCO - A seguito degli approfondimenti trasportistici svolti, e con la finalità di contenere al massimo gli impatti al suolo, si prevede la cessione di aree a parcheggio pubblico per una superficie pari a 9.696 mq. La dotazione di sosta necessaria al funzionamento del compendio immobiliare sarà garantita mediante parcheggi pertinenziali privati realizzati in struttura. Di conseguenza e sulla base di studi tecnici di viabilità e della relativa relazione trasportistica, le aree a parcheggio derivanti dagli obblighi di standard e non reperite a raso saranno compensate mediante la cessione aggiuntiva di aree destinate a Parco Urbano Territoriale, che risulta pertanto incrementato di 11.054 mq, assicurando il rispetto della dotazione complessiva dovuta a standard ma orientando la fruizione pubblica verso una soluzione più coerente sotto il profilo ambientale e paesaggistico.

LEGENDA

┄	Perimetro Ambito

Dotazioni territoriali pubbliche:

🟨	Parco urbano territoriale		
🟧	Parcheggio pubblico	↔	Collegamenti a ciclabili esistenti
🟨	Viabilità pubblica	↔	Collegamenti a ciclabili di possibile sviluppo
○○○○	Percorso ciclopedonale di progetto	○○○○	Percorso ciclopedonale esistente

ACCORDO DI PROGRAMMA
RIGENERAZIONE URBANA E TERRITORIALE DELL'EX AMBITO ESTRATTIVO DEL PADERGNONE
NUOVO POLO TECNOLOGICO DI INTERESSE SOVRALOCALE

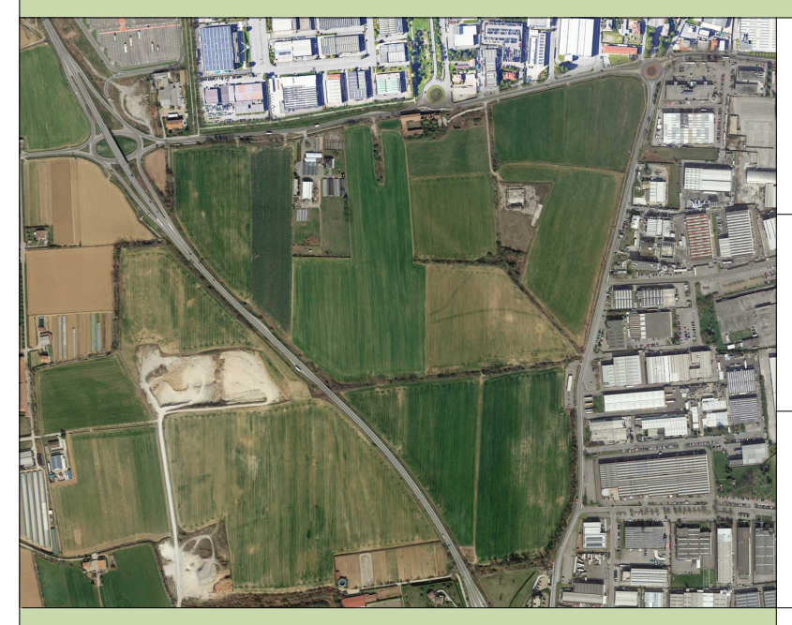

PROVINCIA DI BERGAMO
Via Torquato Tasso 8
24121 Bergamo
PEC protocollo@pec.provincia.bergamo.it
Tel 035387111

COMUNE DI ZANICA
Via Roma 35
24050 Zanica
PEC protocollo@pec.comune.zanica.bg.it
Tel 0354245811

PROMOTORE
Real Estate SPV Project 2415 S.r.l.
Corso Vittorio Emanuele II No. 24/28
20122 – Milano (Italia)
PEC realestatespvproject2415@legalmail.it
Tel +39 02 7788051 -

D - PIANIFICAZIONE ATTUATIVA

SCALA 1:1000

DATA SETTEMBRE 2026

TITOLO TAVOLA
STANDARD URBANISTICI DI PIANO:
AREE IN CESSIONE AL COMUNE

NUMERO TAVOLA **D5.1**

AGGIORN.
AGGIORN.
AGGIORN.

N

TAVOLO TECNICO ISTITUZIONALE

COMUNE DI ZANICA:
UFFICIO URBANISTICA EDILIZIA PRIVATA E SUE
Dirigente
Dott. arch. Gianluca Della Mea
gianluca.dellamea@comune.zanica.bg.it
tel. 035 4245811 int 3

PROGETTISTI E CONSULENTI

PROGETTO URBANISTICO E COORDINAMENTO GENERALE
Marcello Fiorina - ingegnere
Elisabetta Nani - ingegnere
Studio associato di architettura urbanistica ed ingegneria
Sede in via pignolo 5, Bergamo tel 035-218094 - 035-270308
www.studiofiorina.com - indirizzo email: info@studiofiorina.com

PAESAGGIO AMBIENTE E NATURA
STUDIO GERUNDO
Studio Gerundo
Arch. Paolo Pelliccioli
Ing. Susanna Quirico
Dott. Agr. Alberto Massa Saluzzo
Via Cagnola 25 – Treviglio
Tel 3475331955 e-mail: info@studiogerundo.it

RKD
Kevin Maguire
Derek Meenan
The Eight Building
Dublin - Ireland - D08 T2TX
Tel +353 1 668 1055 e-mail: mail@rkd.ie
https://www.rkd.ie

BEAST Design Studios GmbH
Gustavo Espigado
Kölner Str. 1
Eschborn - Germany - 65760
Tel +49 (0) 6196 7700 410
e-mail: g.espigado@beastdesignstudios.com
www.beastdesignstudios.com

ETS Engineering and Technical Services SpA
Donato Romano
Via Angelo Mazzi, 32
Villa d'Almè - Bergamo - 24018
Tel +39 035 6313111 e-mail: info@etseng.it
https://www.etseng.it/

TRASPORTI, AMBIENTE, INVARIANZA IDRAULICA
TE.A. CONSULTING SRL
ING. MASSIMO MOI
MI Via G.B. Grassi 15 - 20157 Milano (MI)
T 02 21711067
BG Via Don A. Mazzucotelli 6 - 24020 Gorle (BG)
T 035 321360
www.territorioambiente.com

VALUTAZIONE AMBIENTALE STRATEGICA
TE.A. CONSULTING SRL
ING. MASSIMO MOI
MI Via G.B. Grassi 15 - 20157 Milano (MI)
T 02 21711067
BG Via Don A. Mazzucotelli 6 - 24020 Gorle (BG)
T 035 321360
www.territorioambiente.com

H&MV Engineering
Paul O'Helleran, Fabio Sbacches
Hamilton House Block 2
Castletroy - Ireland - V94 YHD6
Tel +35 36 135 7496 e-mail: info@hmvengineering.com
https://www.hmvengineering.com/