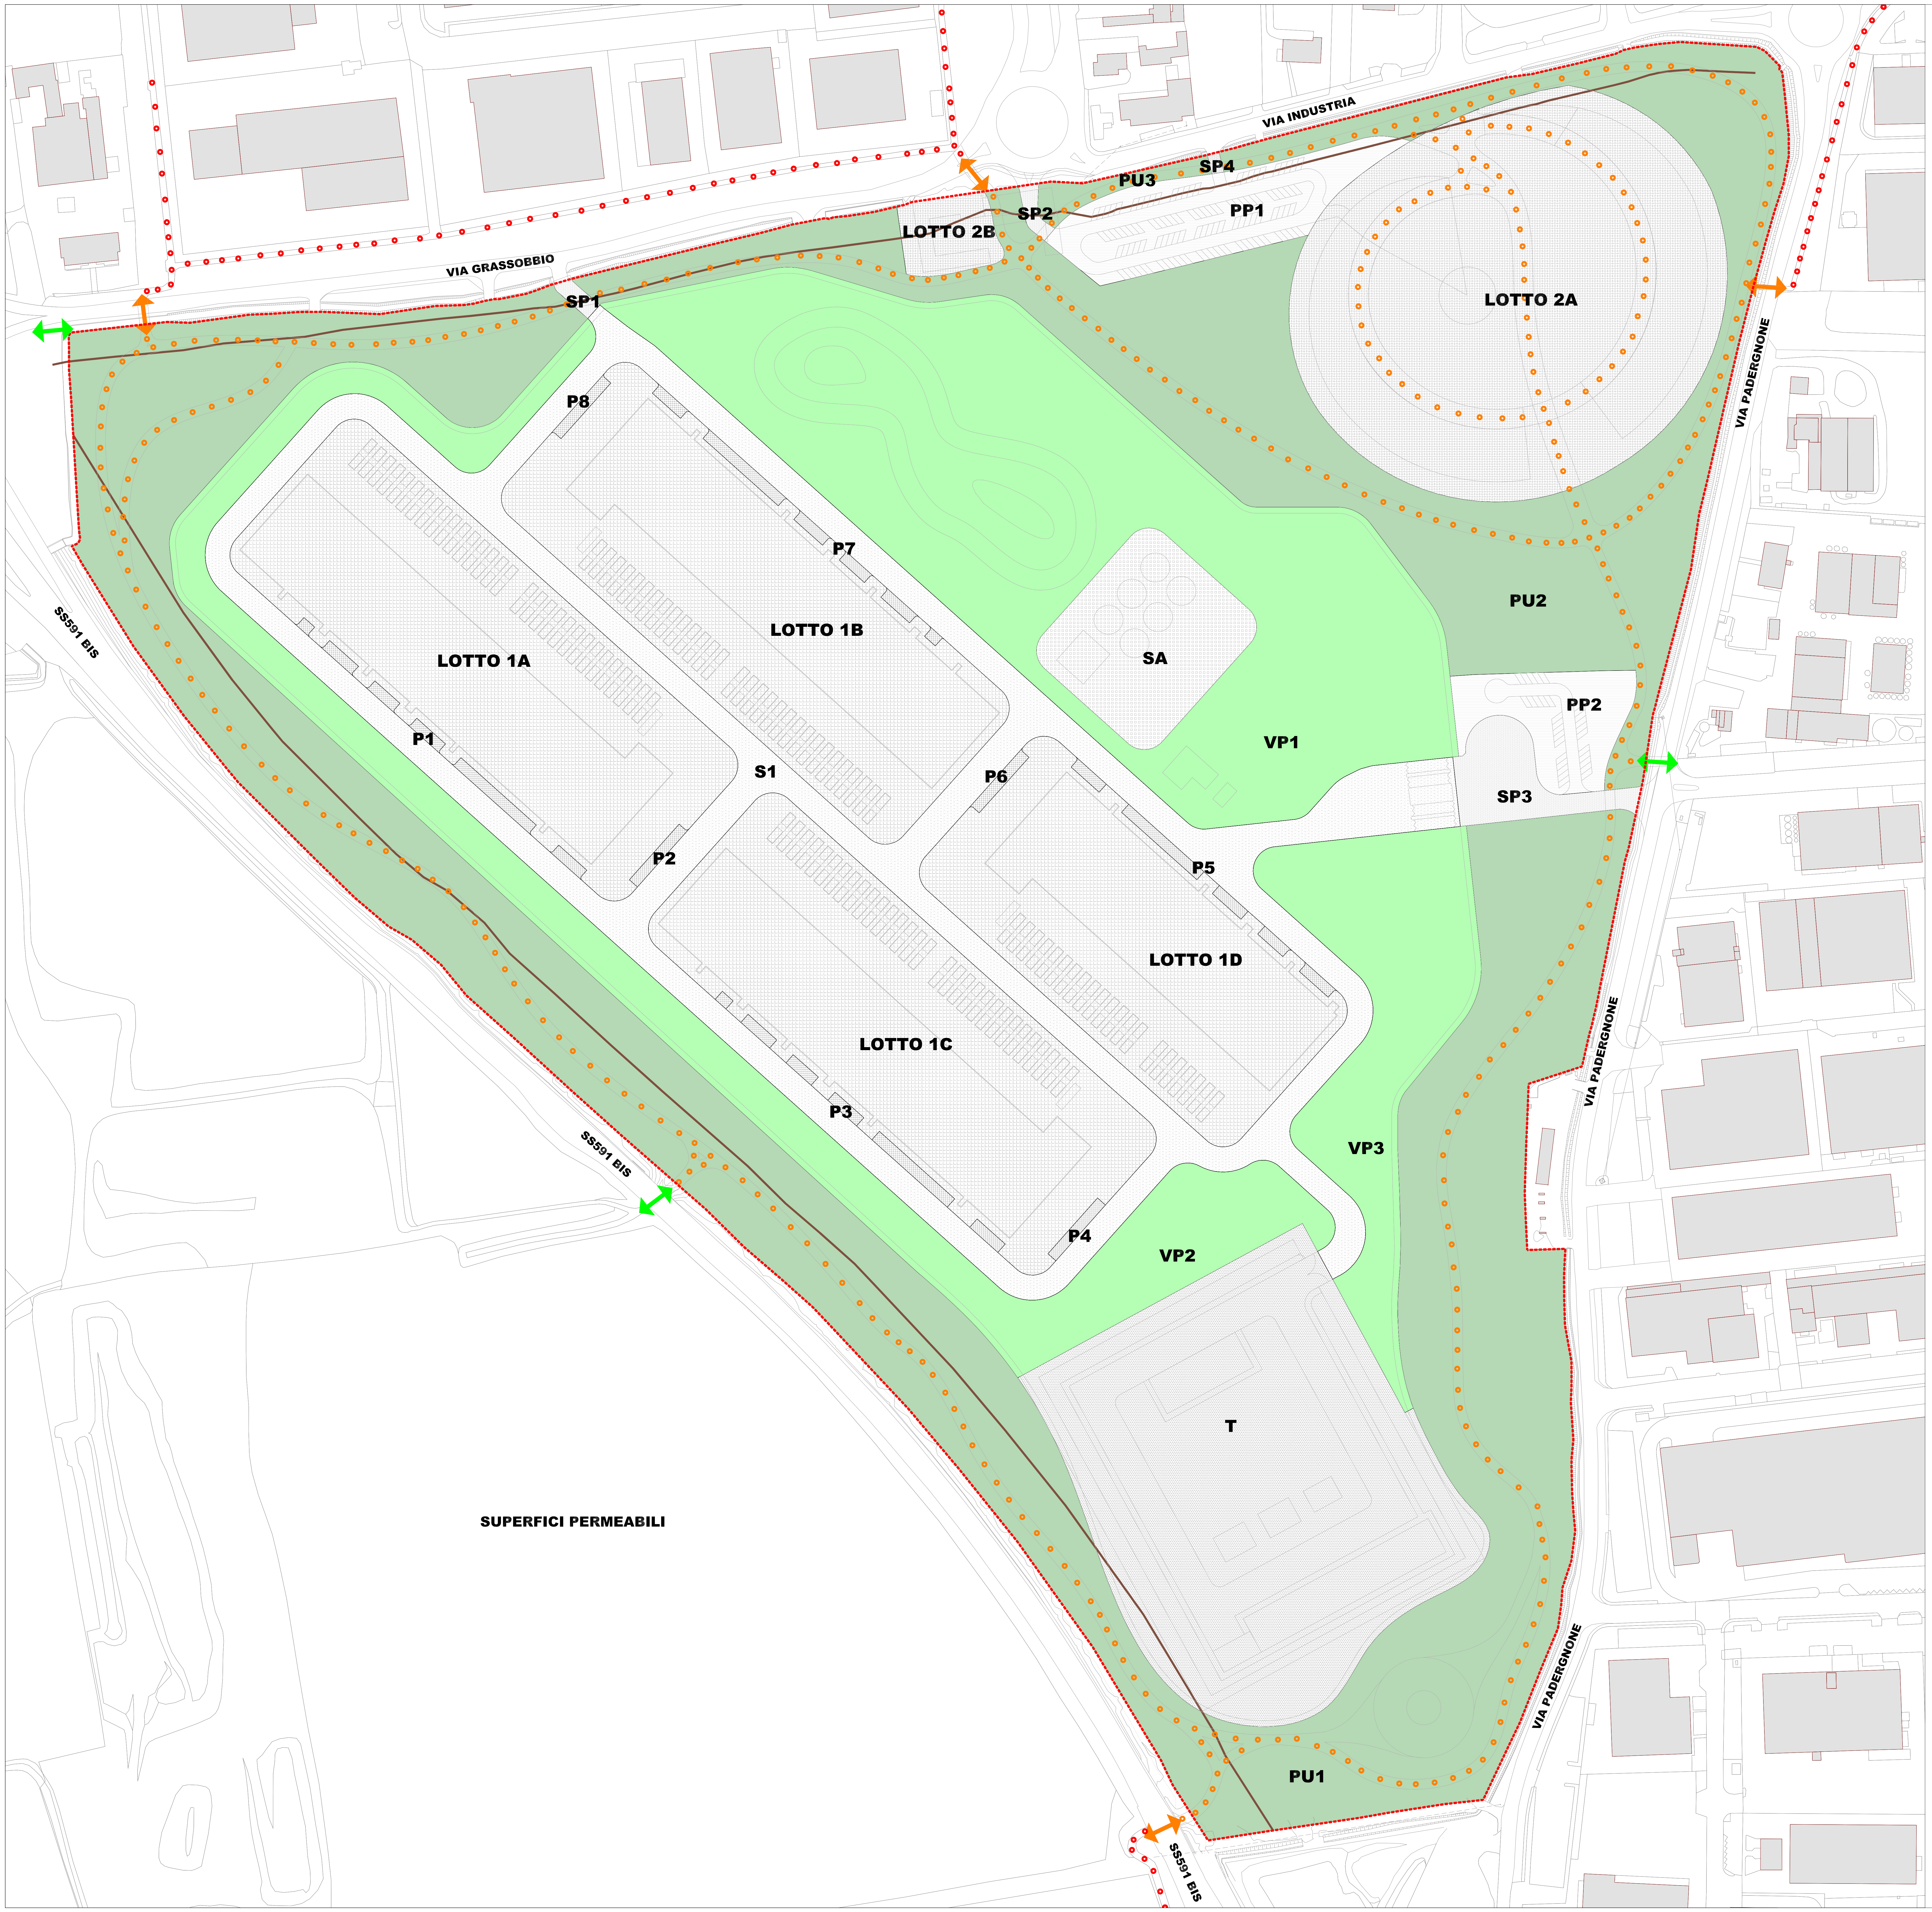

VERIFICA DOTAZIONE SUPERFICIE PERMEABILI	ST (mq)				Permeabile
		Permeabile da regolamento edilizio			
Superficie territoriale generale dell'intervento	437.637	15%	65.646		
		Permeabile da PGT			Garantita
Superficie territoriale generale dell'intervento	437.637	30%	**131.291**	<	**215.046**
Aree verdi private (VP1-VP2-VP3)					82.303
Parco urbano territoriale (PU1-PU2-PU3)					132.743
Totale aree permeabili garantite					**215.046**
Totale aree permeabili garantite in % sulla ST		**30,0%**	<		**49,1%**

NB. Oltre alle aree permeabili indicate, all'interno della zona Tech Hub potranno essere realizzate ulteriori aree permeabili che andranno a migliorare ulteriormente il parametro complessivo

VERIFICA AREE LIBERE PER RIDUZIONE CONSUMO DI SUOLO	mq.
Superficie di suolo libero minima da garantire nel Piano (da scheda PGT)	**120.000**
	<
Superficie suolo libero garantita (Parco urbano territoriale PU1-PU2-PU3)	**132.743**

LEGENDA

┄	Perimetro Ambito

SUPERFICI PERMEABILI

🟩	Superficie permeabile pubblica	↔	Collegamenti a ciclabili esistenti
🟩	Superficie permeabile privata	↔	Collegamenti a ciclabili di possibile sviluppo
••••	Percorso ciclopedonale di progetto	••••	Percorso ciclopedonale esistente

ACCORDO DI PROGRAMMA

RIGENERAZIONE URBANA E TERRITORIALE DELL'EX AMBITO ESTRATTIVO DEL PADERGNONE

NUOVO POLO TECNOLOGICO DI INTERESSE SOVRALOCALE

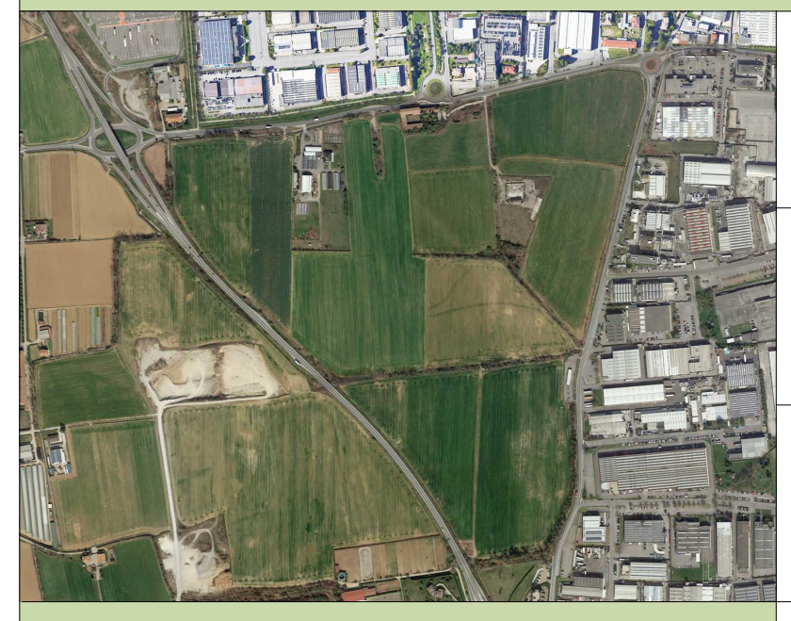

PROVINCIA DI BERGAMO
Via Torquato Tasso 8
24121 Bergamo
PEC protocollo@pec.provincia.bergamo.it
Tel 035387111

COMUNE DI ZANICA
Via Roma 35
24050 Zanica
PEC protocollo@pec.comune.zanica.bg.it
Tel 0354245811

PROMOTORE
Real Estate SPV Project 2415 S.r.l.
Corso Vittorio Emanuele II No. 24/28
20122 – Milano (Italia)
PEC realestatespvproject2415@legalmail.it
Tel +39 02 7788051 -

D - PIANIFICAZIONE ATTUATIVA

	SCALA 1:2000	DATA SETTEMBRE 2026	
TITOLO TAVOLA **SUPERFICI PERMEABILI**	NUMERO TAVOLA **D5.2**	AGGIORN. AGGIORN. AGGIORN.	N

TAVOLO TECNICO ISTITUZIONALE

COMUNE DI ZANICA:
UFFICIO URBANISTICA EDILIZIA PRIVATA E SUE
Dirigente
Dott. arch. Gianluca Della Mea
gianluca.dellamea@comune.zanica.bg.it
tel. 035 4245811 int 3

PROGETTISTI E CONSULENTI

PROGETTO URBANISTICO E COORDINAMENTO GENERALE

Marcello Fiorina - ingegnere
Elisabetta Nani - ingegnere
Studio associato di architettura urbanistica ed ingegneria
Sede in via pignolo 5, Bergamo tel 035-218094 - 035-270308
www.studiofiorina.com - indirizzo email: info@studiofiorina.com

PAESAGGIO AMBIENTE E NATURA

Studio Gerundo
Arch. Paolo Pellicciolì
Ing. Susanna Quirico
Dott. Agr. Alberto Massa Saluzzo
Via Cagnola 25 – Treviglio
Tel 3475331955 e-mail: info@studiogerundo.it

RKD
Kevin Maguire
Derek Meenan
The Eight Building
Dublin - Ireland - D08 T2TX
Tel +353 1 668 1055 e-mail: mail@rkd.ie
https://www.rkd.ie

BEAST Design Studios GmbH
Gustavo Espigado
Kölner Str. 1
Eschborn - Germany - 65760
Tel +49 (0) 6196 7700 410
e-mail: g.espigado@beastdesignstudios.com
www.beastdesignstudios.com

ETS Engineering and Technical Services SpA
Donato Romano
Via Angelo Mazzi, 32
Villa d'Almè - Bergamo - 24018
Tel +39 035 6313111 e-mail: info@etseng.it
https://www.etseng.it/

TRASPORTI, AMBIENTE, INVARIANZA IDRAULICA

TE.A. CONSULTING SRL
ING. MASSIMO MOI
MI Via G.B. Grassi 15 - 20157 Milano (MI)
T 02 21711067
BG Via Don A. Mazzucotelli 6 - 24020 Gorle (BG)
T 035 321360
www.territorioambiente.com

VALUTAZIONE AMBIENTALE STRATEGICA

TE.A. CONSULTING SRL
ING. MASSIMO MOI
MI Via G.B. Grassi 15 - 20157 Milano (MI)
T 02 21711067
BG Via Don A. Mazzucotelli 6 - 24020 Gorle (BG)
T 035 321360
www.territorioambiente.com

H&MV Engineering
Paul O'Helleran, Fabio Sbacches
Hamilton House Block 2
Castletroy - Ireland - V94 YHD6
Tel +35 36 135 7496 e-mail: info@hmvengineering.com
https://www.hmvengineering.com/